

ДОПОЛНИТЕЛЬНОЕ СОГЛАШЕНИЕ №2
к Договору подряда №37-СФ от 15.08.2025

г. Москва

15.08.2025

Общество с ограниченной ответственностью «ВБ Инжиниринг» (ООО «ВБ Инжиниринг»), именуемое в дальнейшем **«Заказчик»**, в лице генерального директора Куликова Алексея Альбертовича, действующего на основании Устава, с одной стороны, и

Общество с ограниченной ответственностью «МОНТПЛАН», именуемое в дальнейшем **«Подрядчик»**, в лице генерального директора Папуца Александра Ивановича, действующего на основании Устава, с другой стороны, далее именуемые **«Стороны»**, заключили настоящее Дополнительное соглашение (далее – Соглашение) к Договору подряда №37-СФ от 15.08.2025 (далее – Договор) о нижеследующем:

1. Стороны договорились, что в рамках действия Договора Подрядчик выполняет объем работ на объекте: **«Логистический комплекс, расположенный по адресу: город Москва поселение Краснопахорское, квартал №147, земельный участок 1Д»**, в соответствии с Техническим заданием (Приложение № 1 к настоящему Соглашению), а Заказчик обязуется оплатить его.
2. Стоимость Работ, выполняемых Подрядчиком в рамках настоящего Соглашения, согласована Сторонами в Локальном сметном расчете (Приложение № 2 к настоящему Соглашению).
3. Оплата работ по настоящему дополнительному соглашению осуществляется Заказчиком в порядке и сроки, установленных Графиком финансирования (Приложение № 4 к настоящему Соглашению).
4. Работы, согласованные Сторонами, подлежат выполнению Подрядчиком в сроки, установленные в Графике производства работ (Приложение № 3 к настоящему Соглашению).
5. Во всем остальном, что не предусмотрено настоящим Соглашением, Стороны руководствуются условиями Договора.
6. Настоящее Соглашение и приложения к нему действуют с момента их подписания Сторонами.
7. Настоящее Соглашение и все Приложения к нему являются неотъемлемой частью Договора.

Приложения:

Приложение № 1: Техническое задание.

Приложение № 2: Локальный сметный расчет.

Приложение № 3: График производства работ.

Приложение № 4: График финансирования.

Приложение № 5: Акт приема-передачи строительной площадки.

АДРЕСА, БАНКОВСКИЕ РЕКВИЗИТЫ И ПОДПИСИ СТОРОН

Заказчик:

ООО «ВБ Инжиниринг»

Юридический адрес: 142181, Московская область,

Г.О. Подольск, г. Подольск, д. Коледино,

тер. Индустриальный парк Коледино, д. 6, стр. 1

ИНН/КПП 5074085992/507401001

ОГРН 1235000163111

E-mail: wbi@wildberries.ru

Подрядчик:

ООО «Монтплан»

Юридический адрес: 119049, г. Москва, ул.

Мытная, д. 28, стр. 3, этаж 1 пом. 2, ком. 3, оф. 20

ИНН/КПП 7706807342/770601001

ОГРН 1147746267470

E-mail: info@montplan-ooo.ru

Генеральный директор

_____/ **А.А. Куликов/**

М.П.

Генеральный директор

_____/ **А.И. Папуца/**

М.П.



ТЕХНИЧЕСКОЕ ЗАДАНИЕ

Устройство фундамента котельной и дымовых труб

1. Наименование объекта	Логистический комплекс, расположенный по адресу: город Москва поселение Краснопахорское, квартал №147, земельный участок 1Д
2. Адрес участка производства работ	город Москва поселение Краснопахорское, квартал №147, земельный участок 1Д, кадастровый номер 77:22:0020330:1889
3. Вид работ	Устройство монолитных железобетонных цокольных панелей
4. Цель работ	Устройство монолитного железобетонного цоколя
5. Объем и перечень работ	Объем и перечень работ включает, но не ограничивается составом, перечисленным ниже. Работы выполняются Подрядчиком в полном объеме, «под ключ», силами, средствами и механизмами Подрядчика, включая все необходимые расходные материалы и сопутствующие работам расходы. 1. Ведомость объемов работ согласно Рабочей документации и Локальному сметному расчету. 2. Закупка, и доставка расходных материалов, монтажных деталей, материалов для заделки швов и прочих необходимых для работ материалов. 3. Доставка и разгрузка материалов в месте проведения работ. Входной контроль качества с записью в журнале и актах. 4. Мобилизация всей необходимой техники и инструмента на площадку проведения работ в количестве необходимом для качественного проведения работ в соответствии с ГПР. 5. Земляные работы, подготовка основания, утепление. 6. Выполнить устройство монолитных ЖБ конструкций в соответствии с указаниями Рабочей документации. 7. Выполнить неразрушающий контроль прочности монолитных конструкций (освидетельствование конструкций). 8. Выполнить гидроизоляцию соприкасающихся с грунтом поверхностей холодной битумной мастикой в 2 слоя. Выполнить заделку швов. 9. Выполнить утепление цокольных панелей 10. Обратная засыпка песком ср.крупности с послойным уплотнением 11. Передача комплекта Исполнительной документации и сдача работ 12. Иные работы, необходимые для успешного выполнения работ. 13. Демобилизация. По решению Заказчика, часть или полный объем материалов, перечисленный в Ведомости объемов работ, могут быть поставлены Заказчиком, в качестве давальческого материала. Обязанность, в таком случае, за входной контроль, приемку, разгрузку, перемещение к месту производства работ, комплектность, охрана и сохранность материала и имущества, и т.д., остается на Подрядчике.
6. Исходные данные	Комплект рабочей документации КЖ
7. Требования к проведению работ	1. До начала монтажа выполнить проверочную геодезическую съемку верха конструкций ростверков и колонн на соответствие планового и высотного положений, о сверхнормативных отклонениях и расхождениях с Исполнительной съемкой уведомить Заказчика и Подрядчика. 2. До начала производства работ согласовать ППР и график производства работ с Заказчиком. 3. Оперативный контроль прочности бетона производить косвенными неразрушающими методами контроля (ультразвук и т.д.) согласно ГОСТ 18105-2018, ГОСТ 22690-2015. 4. Контроль качества бетона в конструкциях осуществлять в комплексе косвенными (ультразвук и т.д.) и прямыми (отрыв со скалыванием), не разрушающими методами согласно требований ГОСТ 18105-2018, ГОСТ 22690-2015. 5. Категория поверхности цоколей должна быть не ниже по ГОСТ 13015-2012 - А2 для наружной и видимой внутренней поверхностей внутренних створов. 6. Монолитные элементы должны иметь величины допускаемых



	отклонений не более: - плоскостей на 1 м плоскости в любом направлении 5мм; - по вертикали 15мм на этаж и 1/1000Н на всю высоту здания; - по длине и ширине 20мм; - отклонения в размерах поперечного сечения + 6, - 3мм. 7. Для защиты поверхностей, соприкасающихся с грунтом обратной засыпки, выполнить обмазку холодной битумной мастикой в два слоя по подготовленной поверхности. Гидроизолирующая поверхность не должна иметь шероховатостей и раковин. 8. Укладку, прогрев, и уход за бетоном осуществлять согласно требованиям СП 70.13330.2012, СП 435.1325800.2018. 9. Все работы выполняются «под ключ» материалами и силами Подрядчика. В стоимость работ входит, временное освещение, пункт мойки колес и его обслуживание и проживание и питание персонала, устройство временных дорог, сетей и сооружений, санитарно-бытовых помещений, расходные материалы, нахлесты, перехлесты и стыковки материалов, командировочные расходы, материалы и оборудование для укладки, ухода и прогрева бетона, средства индивидуальной защиты для техники безопасности, чистка снега, водоотведение, сбор, вывоз и утилизация мусора, сохранность материалов, оборудования и имущества, получение и разработка необходимых сопутствующих документов для производства работ и другие затраты, необходимые для успешного выполнения работ в установленные договором сроки и с качеством, соответствующим требованиям Заказчика, настоящего ТЗ и Рабочей документации. 10. При строительстве объекта руководствоваться Приказом Минстроя России от 16.05.2023 N 344/пр в части состава и перечня актов освидетельствования работ и освидетельствования конструкций, комплекта Исполнительной документации. 11. При выполнении работ и после завершения работ необходимо производить уборку территории и вывоз мусора. 12. Любые изменения по составу и содержанию работ, применяемым оборудованию и материалам оформляются документально в письменном виде и направляться к Заказчику на рассмотрение. 13. Оплата выполненных работ производится за фактически выполненный объем работ, на основании исполнительной документации, с подтверждением техническим надзором и геодезистом заказчика. Объемы и стоимость выполненных работ закрываются «в теле», т.е. учет коэфф. уплотнения, разуплотнения, разливов, потерь при транспортировке и при разгрузке/погрузке, нахлестов, обрезков, перехлестов, коэфф. на невосполнимые потери, коэфф. наплавления металла и т.д. должны быть включены в стоимость работ. 14. Подрядчик обязуется подготавливать и направлять Заказчику ежедневный отчет, по форме Заказчика, о выполненных работах. 15. Ежедневно, при выполнении работ, обеспечивать чистоту на строительной площадке и прилегающей территории. После завершения работ необходимо производить уборку территории и вывоз мусора. После завершения работ, привести в порядок и сдать по акту площадки, занятые на время хранения материала и размещения подсобных помещений в строительных городках.
8. Обеспечение электроэнергией	Подрядчик самостоятельно обеспечивает свои потребности в электроэнергии
9. Обеспечение водоснабжением	Подрядчик самостоятельно обеспечивает свои потребности в техническом и хозяйственно-бытовом водоснабжении
10. Перечень нормативно-технических документов, в соответствии с требованиями которых необходимо выполнить работы	1. Работы производить в соответствии с требованиями нормативов: Приказ Минстроя России от 16.05.2023 N 344/пр "Об утверждении состава и порядка ведения исполнительной документации при строительстве, реконструкции, капитальном ремонте объектов капитального строительства". СП 70.13330.2012. Свод правил. Несущие и ограждающие конструкции. Актуализированная редакция СНиП 3.03.01-87. СП 435.1325800.2018. Свод правил. Конструкции бетонные и железобетонные монолитные. Правила производства и приемки работ" СП 45.13330.2017. Свод правил. Земляные сооружения, основания фундаменты. Актуализированная редакция СНиП 3.02.01-87. СП 48.13330.2019 "СНиП 12-01-2004 Организация строительства"



	СП 22.13330.2016. Свод правил. Основания зданий и сооружений. Актуализированная редакция СНиП 2.02.01-83* СП 24.13330.2021. Свод правил. Свайные фундаменты. СНиП 2.02.03-85 ГОСТ Р 21.101-2020. Национальный стандарт Российской Федерации. Система проектной документации для строительства. Основные требования к проектной и рабочей документации ГОСТ 18105-2018. Межгосударственный стандарт. Бетоны. Правила контроля и оценки прочности ГОСТ 22690-2015. Межгосударственный стандарт. Бетоны. Определение прочности механическими методами неразрушающего контроля действующими на территории РФ, Рабочей документацией, Локальным сметным расчетом, Договором и настоящим Техническим заданием, другими техническими и нормативными документами; 2. Используемые материалы, оборудование, инструмент должны соответствовать ГОСТ, ТУ, действующим на территории Российской Федерации, иметь необходимые сертификаты и разрешения. 3. В случае признания утратившими силу нормативно-технических документов, в соответствии с требованиями которых необходимо выполнить работы, указанных в рабочей документации и(или) настоящем Техническом задании, Подрядчик обязан выполнять работы в соответствии с нормативно-техническими документами, принятыми взамен утративших в силу документов.
11. Требования к Охране труда и Технике безопасности	Подрядчик полностью принимает на себя все обязательства по выполнению требований по обеспечению безопасного производства работ, соблюдению требований по ОТ, ТБ и ПБ, в соответствии с требованиями Российского законодательства и провести следующий перечень мероприятий при производстве подрядных работ: организационные мероприятия, технические мероприятия, мероприятия по обеспечению средствами индивидуальной защиты. Перед началом подрядных работ провести инструктажи персонала в области охраны труда и пожарной безопасности с записью в журналах инструктажей. Подрядчик обязан незамедлительно реагировать на все замечания со стороны Заказчика на нарушения правил ОТ, ТБ и ПБ, и незамедлительно устранять их. Заказчик вправе остановить проведение работ подрядчиком до устранения нарушений. Заказчик вправе наложить штраф на Подрядчика за невыполнение требований Заказчика устранить нарушения правил ОТ, ТБ и ПБ.





**ОБЩЕСТВО С ОГРАНИЧЕННОЙ
ОТВЕТСТВЕННОСТЬЮ "ПЦ Град"**

**Свидетельство СРО-П-149-12032010
Заказчик: ООО "ВБ Инжиниринг"**

**"Логистический комплекс, расположенный по адресу: город
Москва, Краснопахорское поселение, вблизи д. Софьино"**

РАБОЧАЯ ДОКУМЕНТАЦИЯ

**Конструкции железобетонные. Часть 5.4.
Фундамент котельной**

4377-2025-Р-КЖ5.4

Директор

О.С. Шипилов

Главный инженер проекта



З.С. Сулейманов

Согласовано		
Взам. инв. №		
Подп. и дата		
Инв. № подл.		


2025




Схема расположения фундаментов

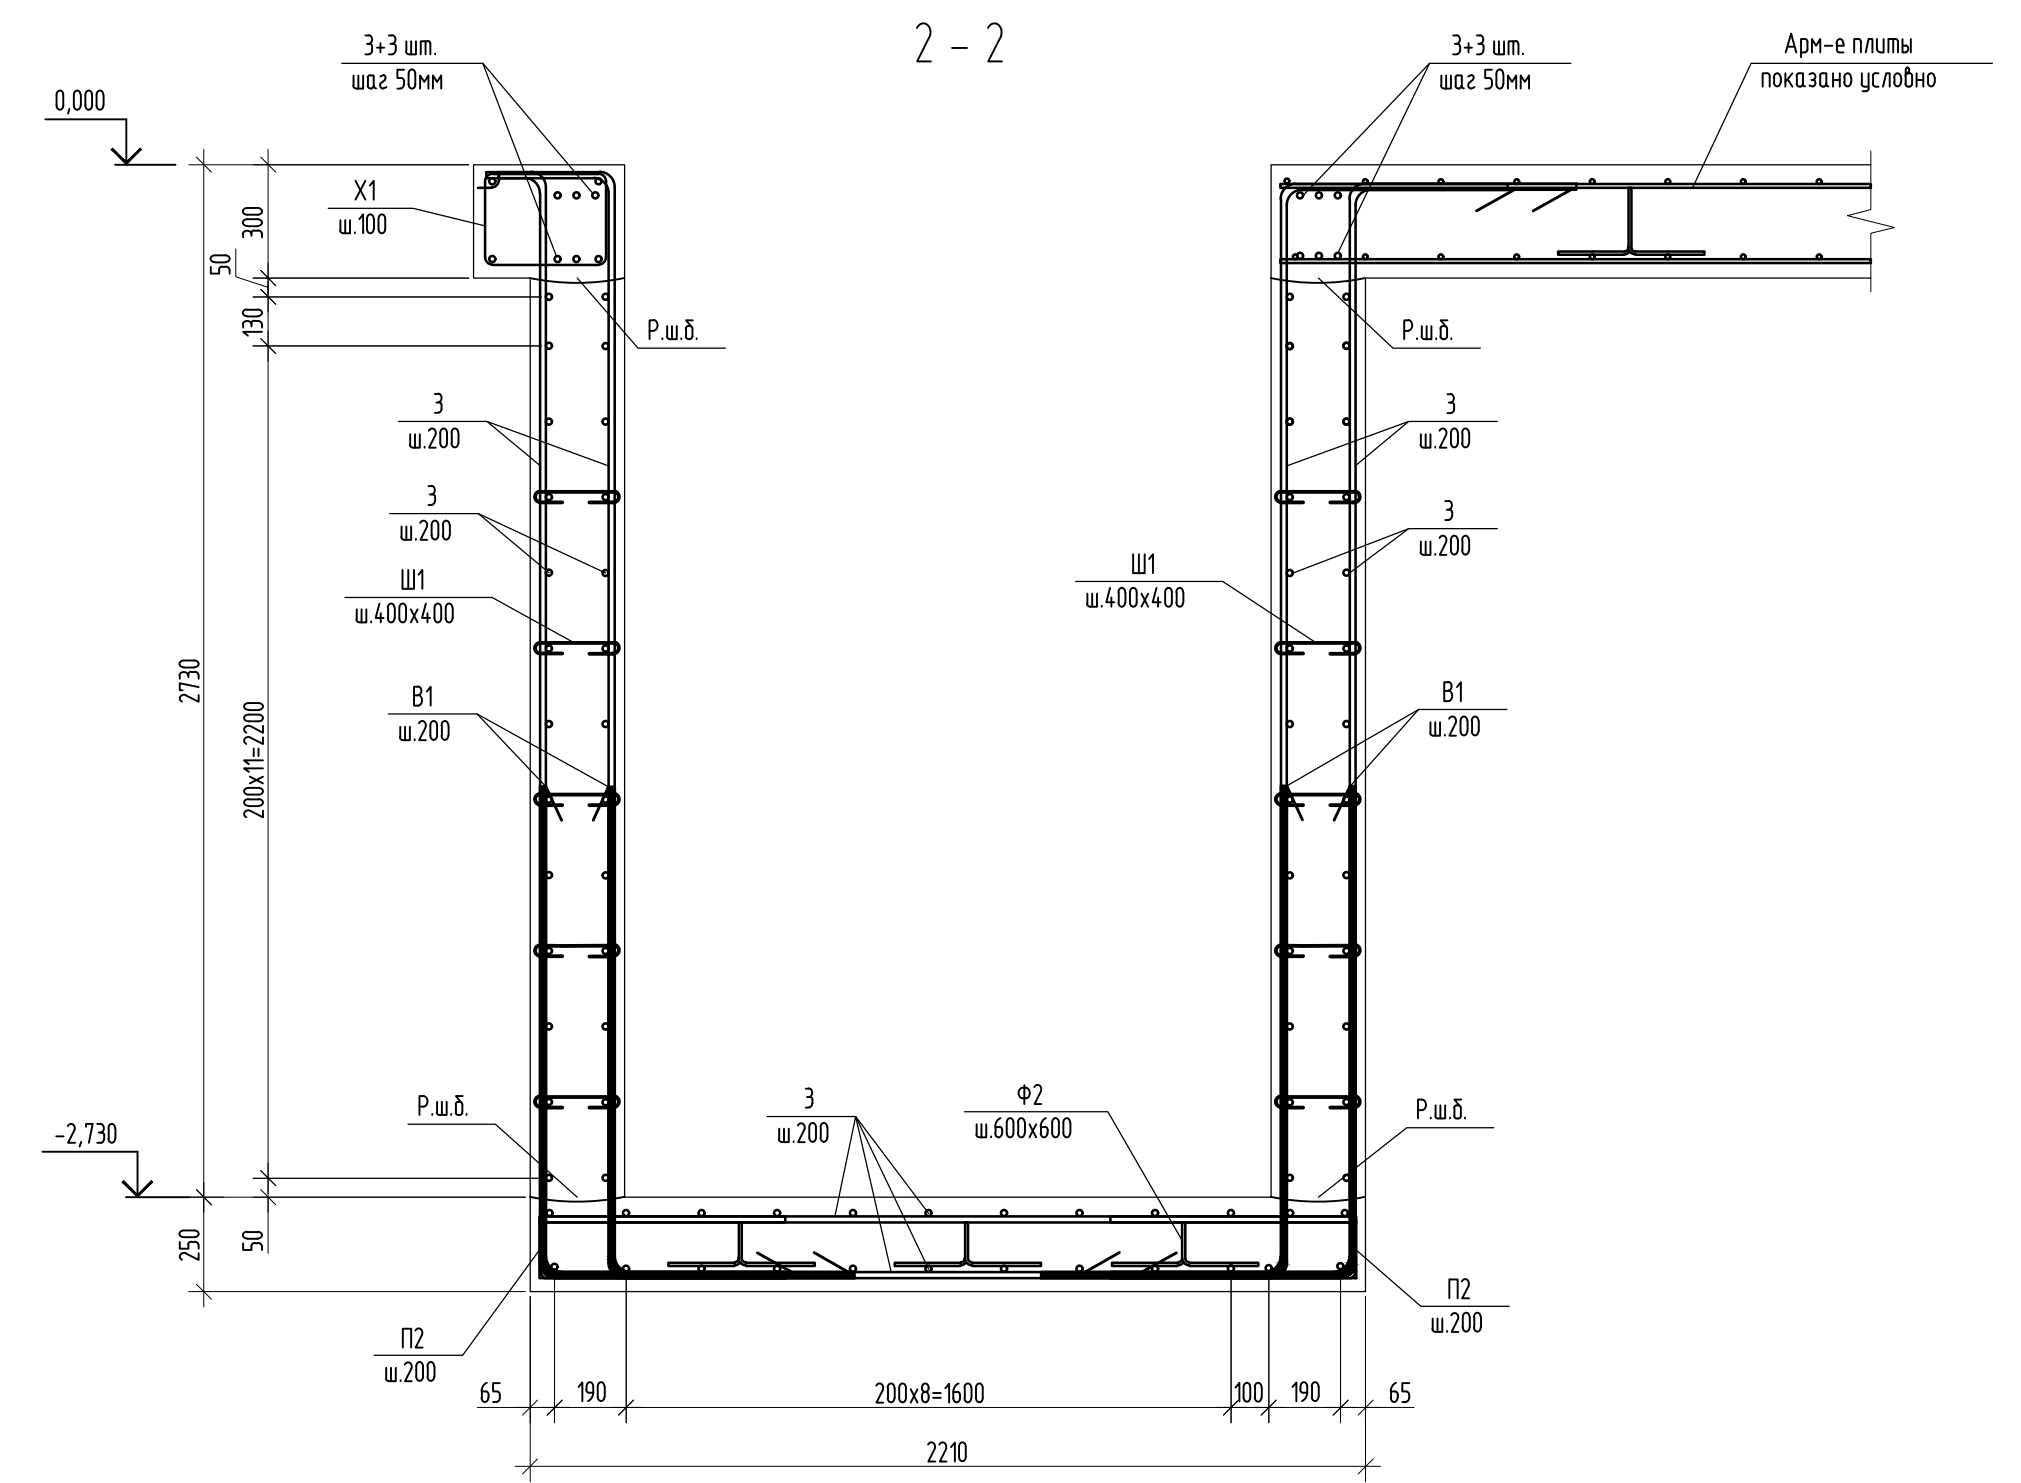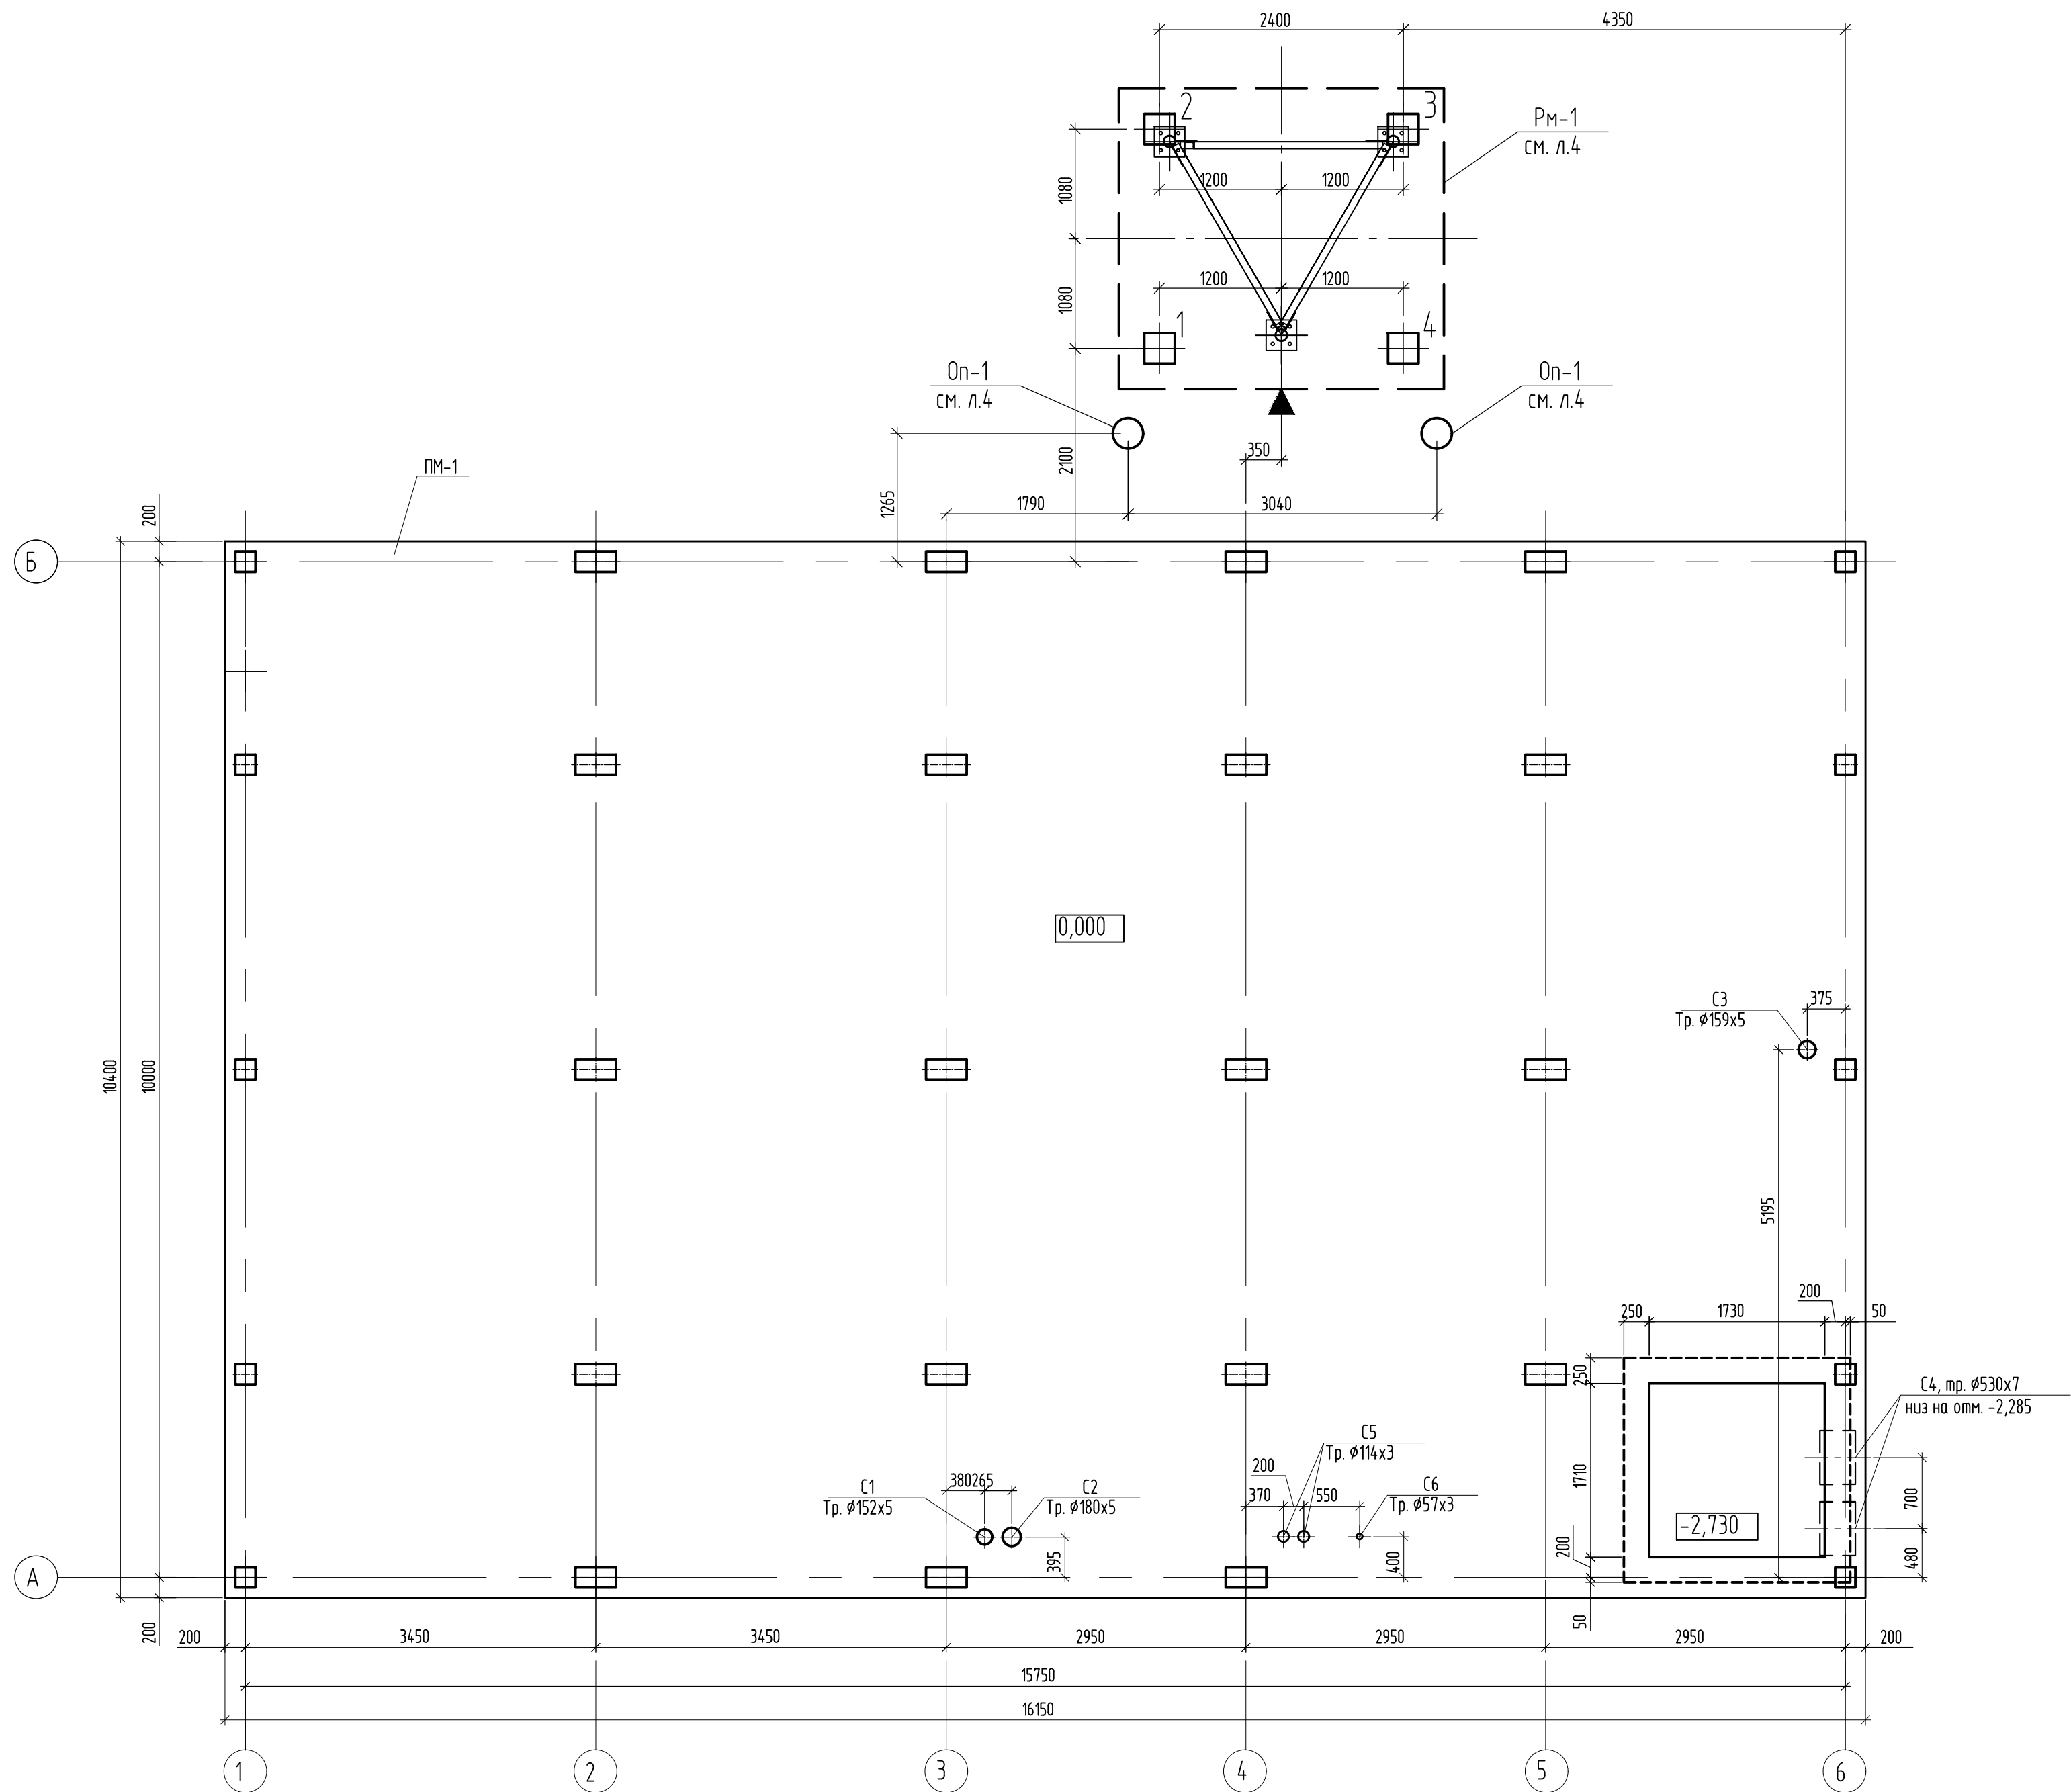[illegible]

Плита монолитная ПМ1. Опалубочный чертёж (1:50)

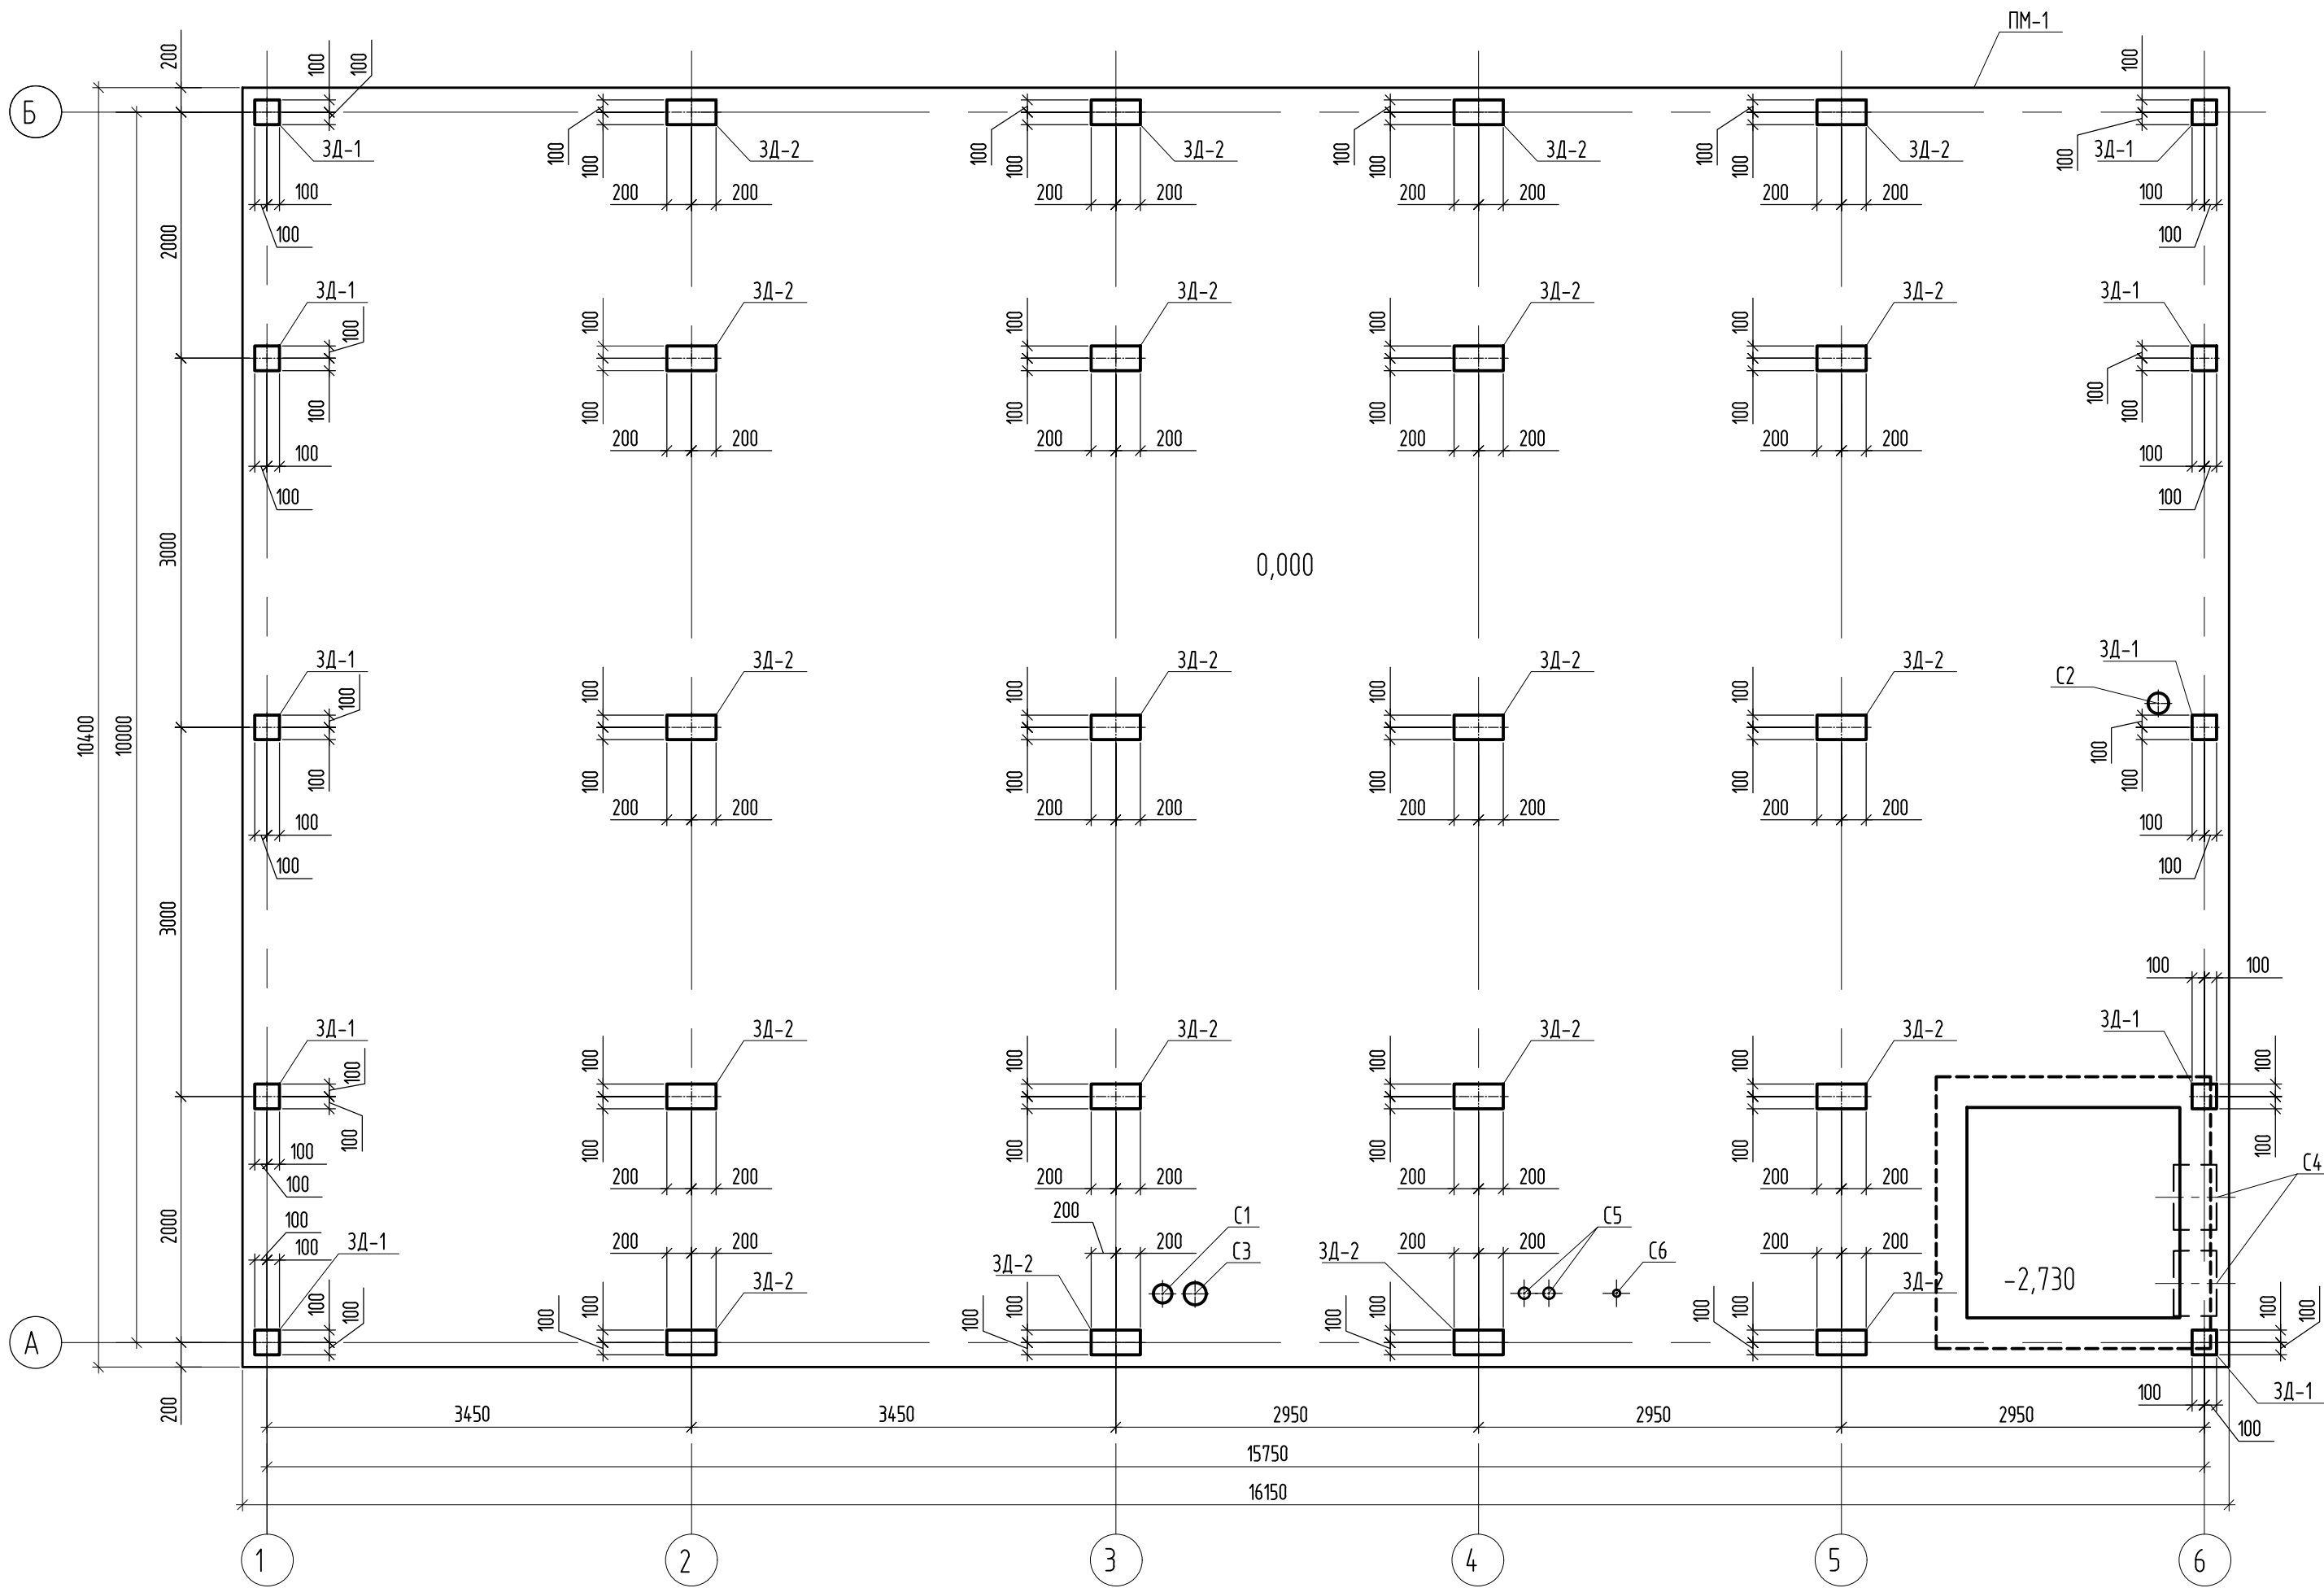

Плита монолитная ПМ1. Схема нижнего и верхнего армирования (1:50)

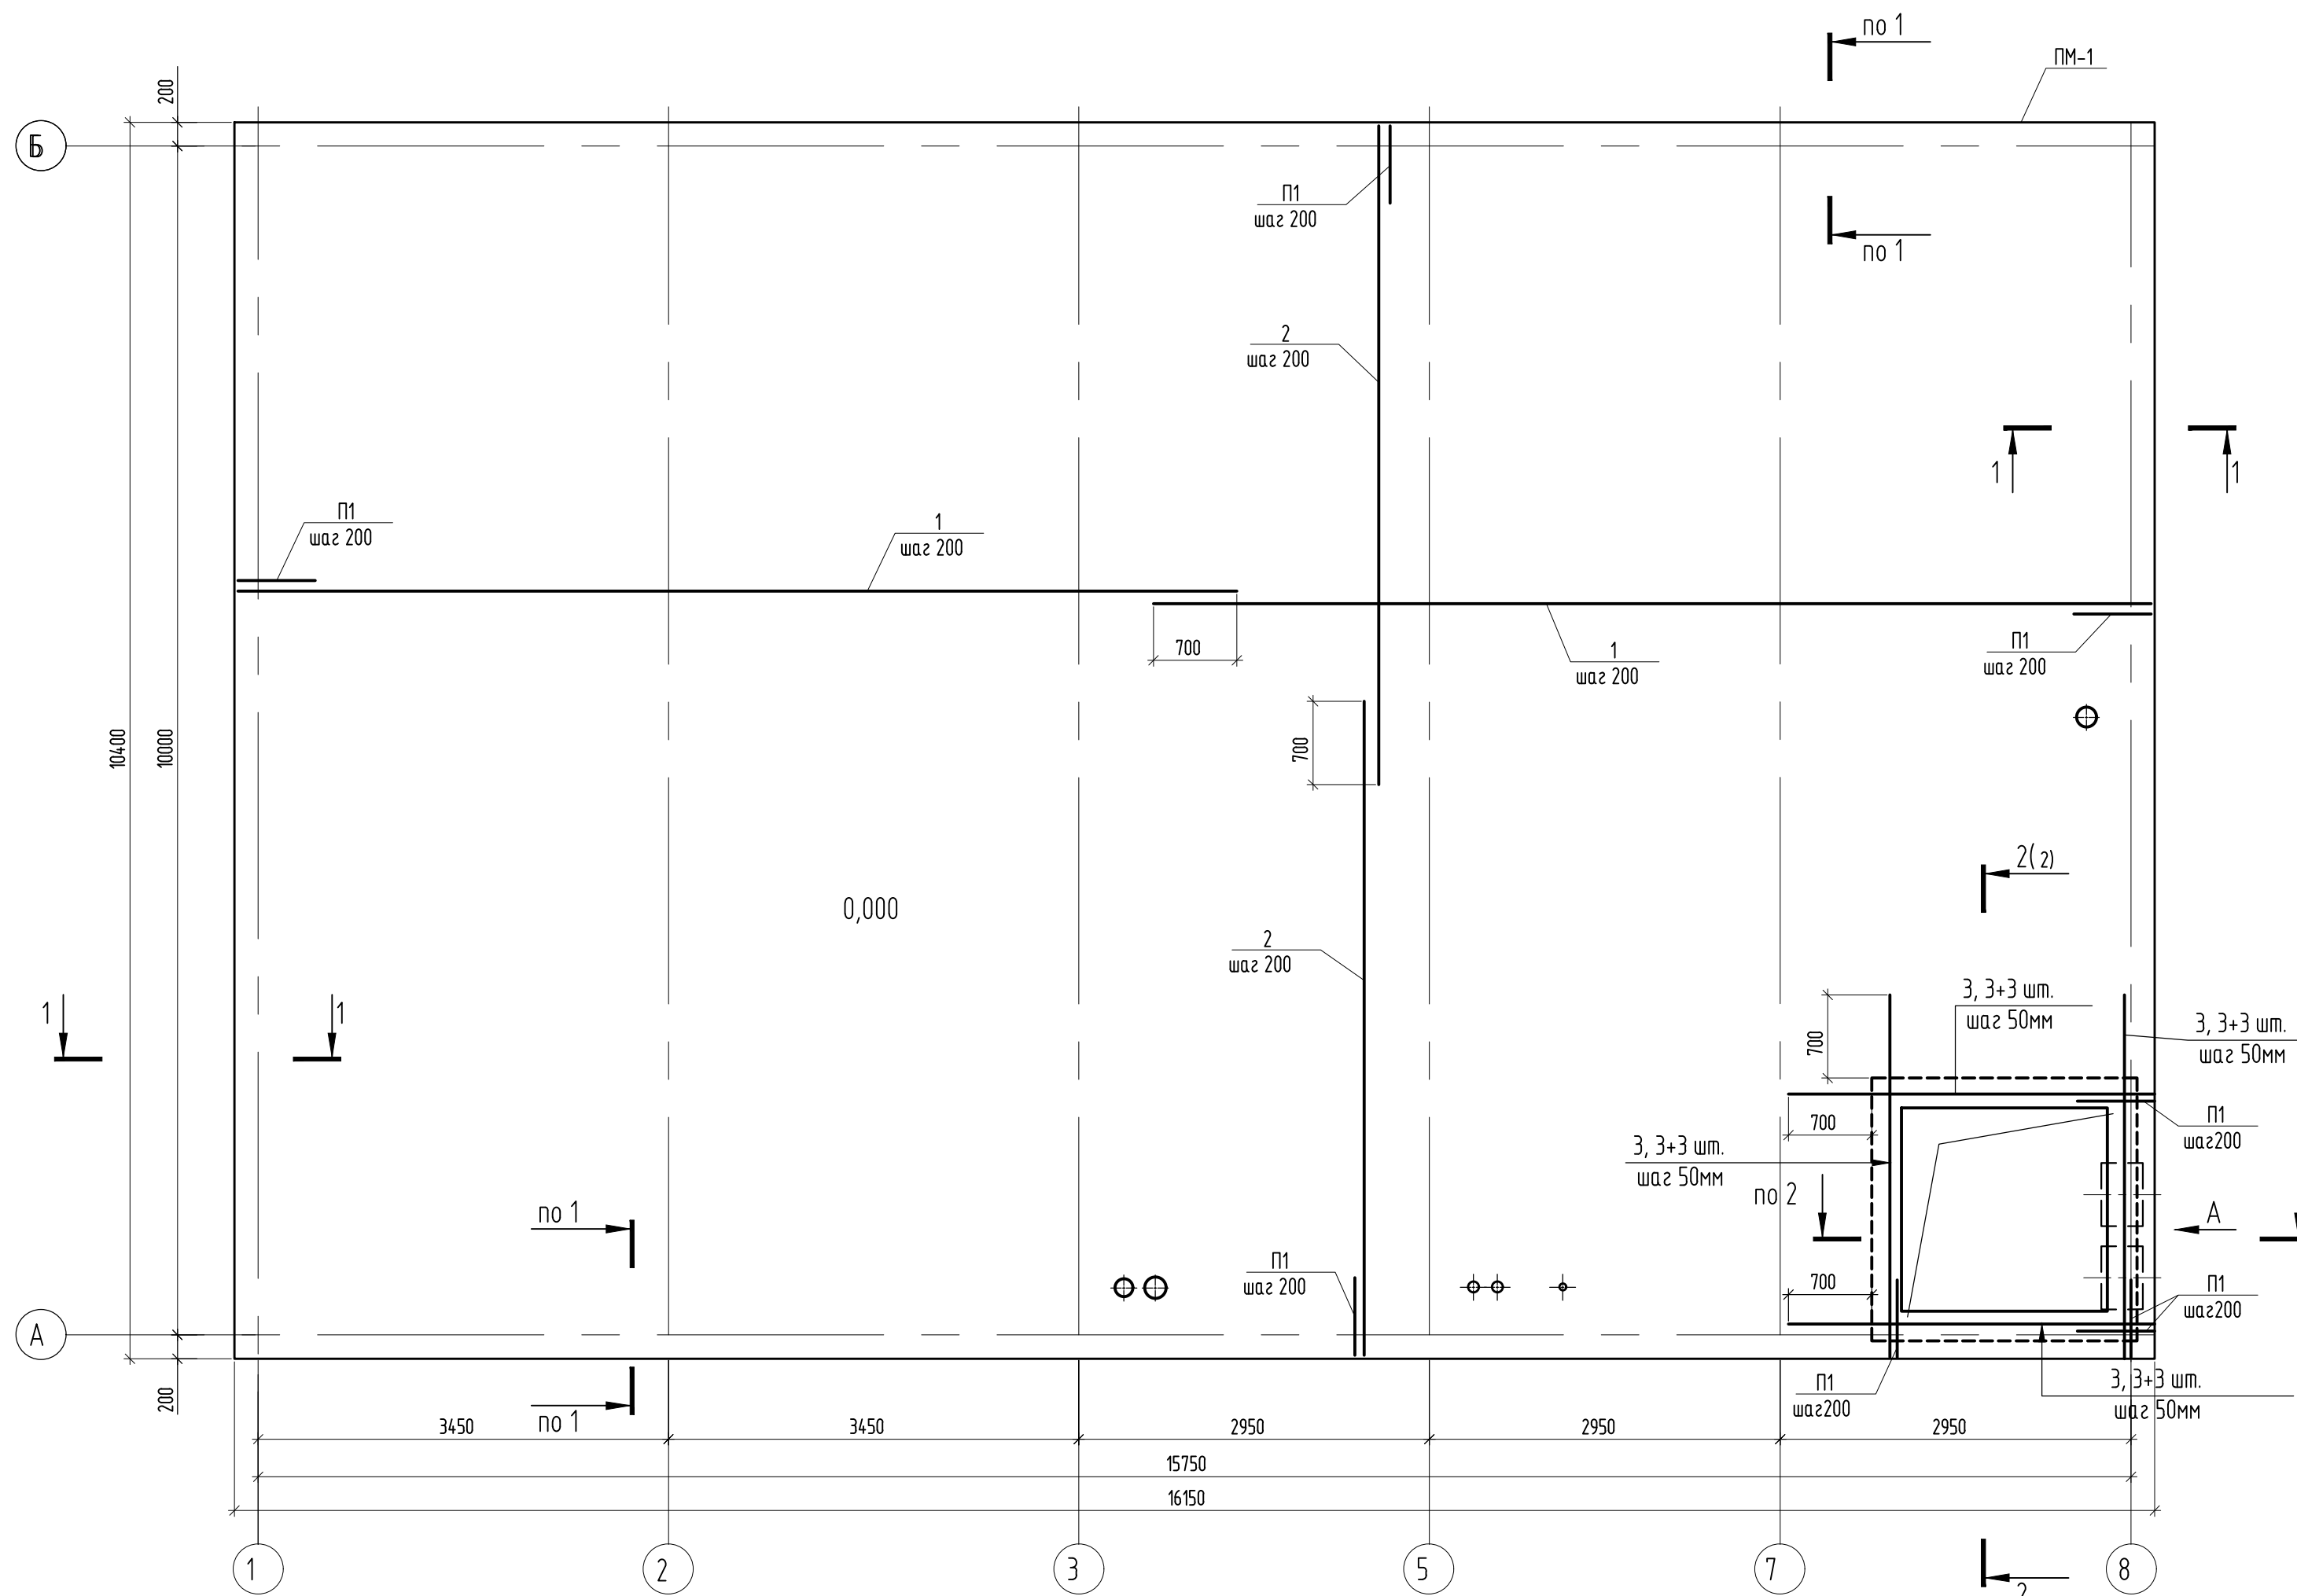

Ведомость деталей плиты ПМ-1

Поз.	Эскиз
П1	
П2	
П3	
Ф1	
Ф2	
В1	
Ш1	
Х1	
Х2	




Спецификация элементов плиты ПМ-1

Поз.	Обозначение	Наименование	Кол.	Масса, ед, кг	Примечание
Изделия					
1	ГОСТ 34028-2016	Ø 14 А500С L= п.м.	1782	1,21	
2	ГОСТ 34028-2016	Ø 14 А500С L= п.м.	1782	1,21	
3	ГОСТ 34028-2016	Ø 16 А500С L= п.м.	715	1,58	
С1	ГОСТ 10704-91	Шляпа Ø152x5,0 l=500мм	1	9,065	
С2	ГОСТ 10704-91	Шляпа Ø159x5,0 l=500мм	1	9,495	
С3	ГОСТ 10704-91	Шляпа Ø180x5,0 l=500мм	2	10,79	
С4	ГОСТ 10704-91	Шляпа Ø530x7,0 l=350мм	2	31,598	
С5	ГОСТ 10704-91	Шляпа Ø114x3,0 l=500мм	2	4,105	
С6	ГОСТ 10704-91	Шляпа Ø57x3,0 l=500мм	1	2	
3В-1	см. л.5	Закапанная деталь 3В-1	10	4,02	
3В-2	см. л.5	Закапанная деталь 3В-2	20	7,6	
Детали					
П1	ГОСТ 34028-2016	Ø 14 А500С L= 1490	287	1,8	
П2	ГОСТ 34028-2016	Ø 16 А500С L= 1490	162	2,352	
П3	ГОСТ 34028-2016	Ø 16 А500С L= 1520	6	2,399	
Ф1	ГОСТ 34028-2016	Ø 8 А500С L= 1290	465	0,509	
Ф2	ГОСТ 34028-2016	Ø 8 А500С L= 1150	8	0,454	
В1	ГОСТ 34028-2016	Ø 16 А500С L= 1850	88	2,92	
Ш1	ГОСТ 34028-2016	Ø 6 А500С L= 330	170	0,073	
Х1	ГОСТ 34028-2016	Ø 6 А500С L= 1190	47	0,264	
Х2	ГОСТ 34028-2016	Ø 6 А500С L= 740	10	0,164	
Материалы					
		Бетон класса В25 F150 W6, нЗ	56,5		
		Бетон класса В7,5, нЗ	18		
		Обмазочная гидроизоляция (1слой)	208		


Спецификация к схеме расположения свай котельной

Номера свай	Условное обозначение	Обозначение	Наименование	Кол.	Масса, ед, кг	Абс. отм., м			Отн. отм., м		
						Верх	Срубка	Низ	Верх	Срубка	Низ
1-4	4#	Серия 10111-10, Вып.1	С80.30-12.У	4	1830	181,20	181,10	173,20	-0,650	-0,750	-8,650

Свай 1-4 устанавливаются на максимальную отметку устройства дымохода. Срубку выполнят перед устройством дымохода. Отметку срубка уточнить в разделе конструкций трубы дымохода.

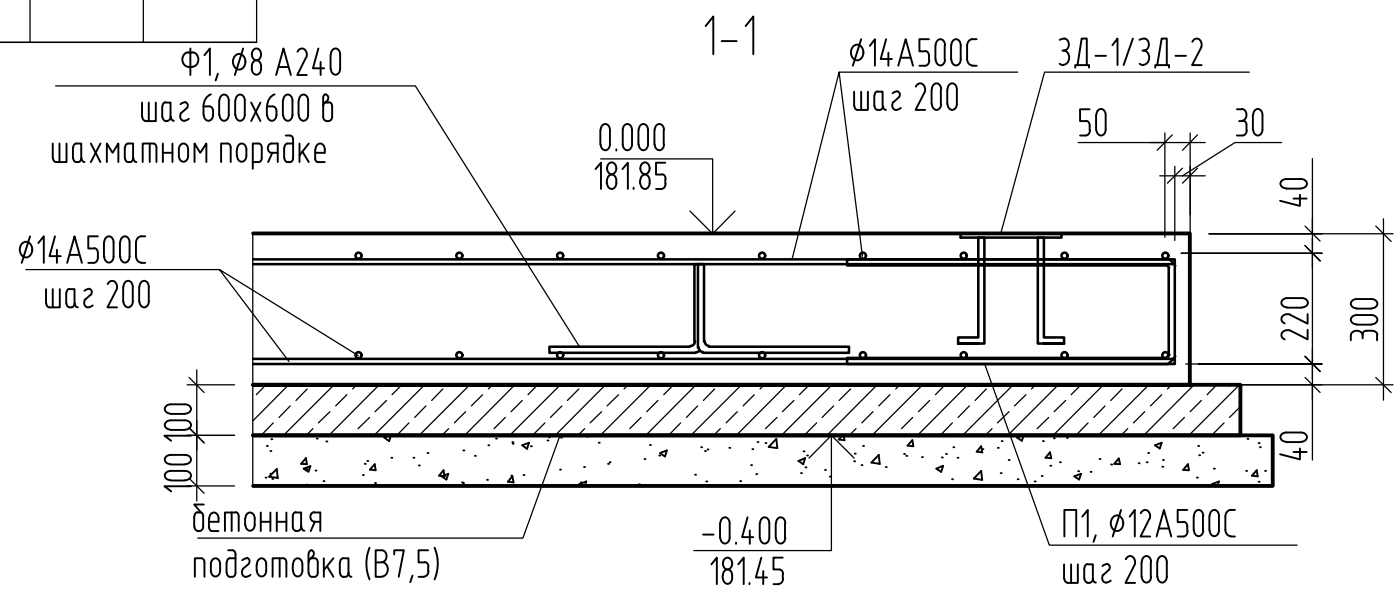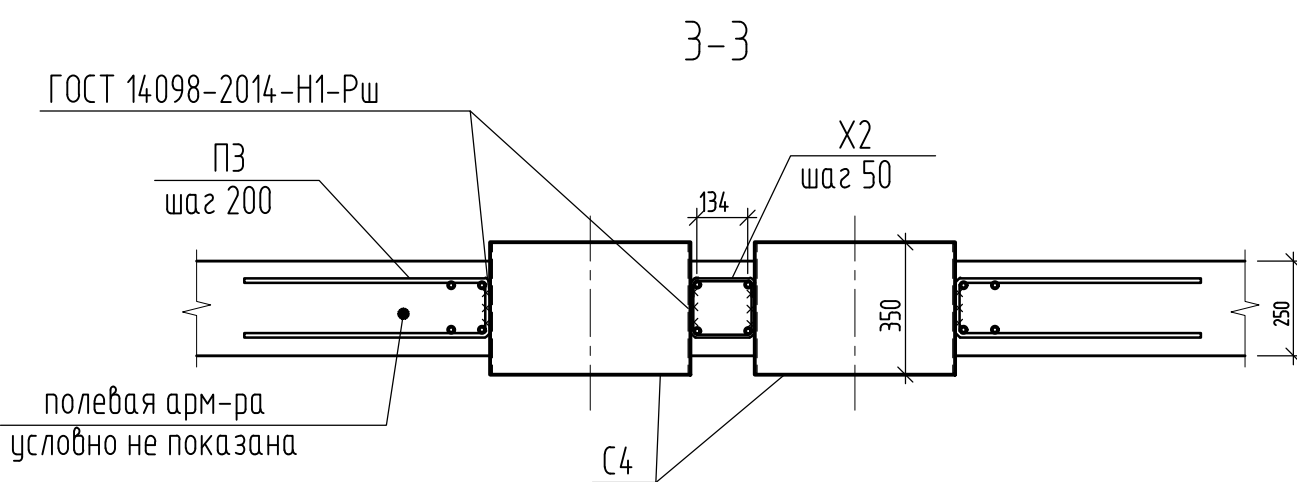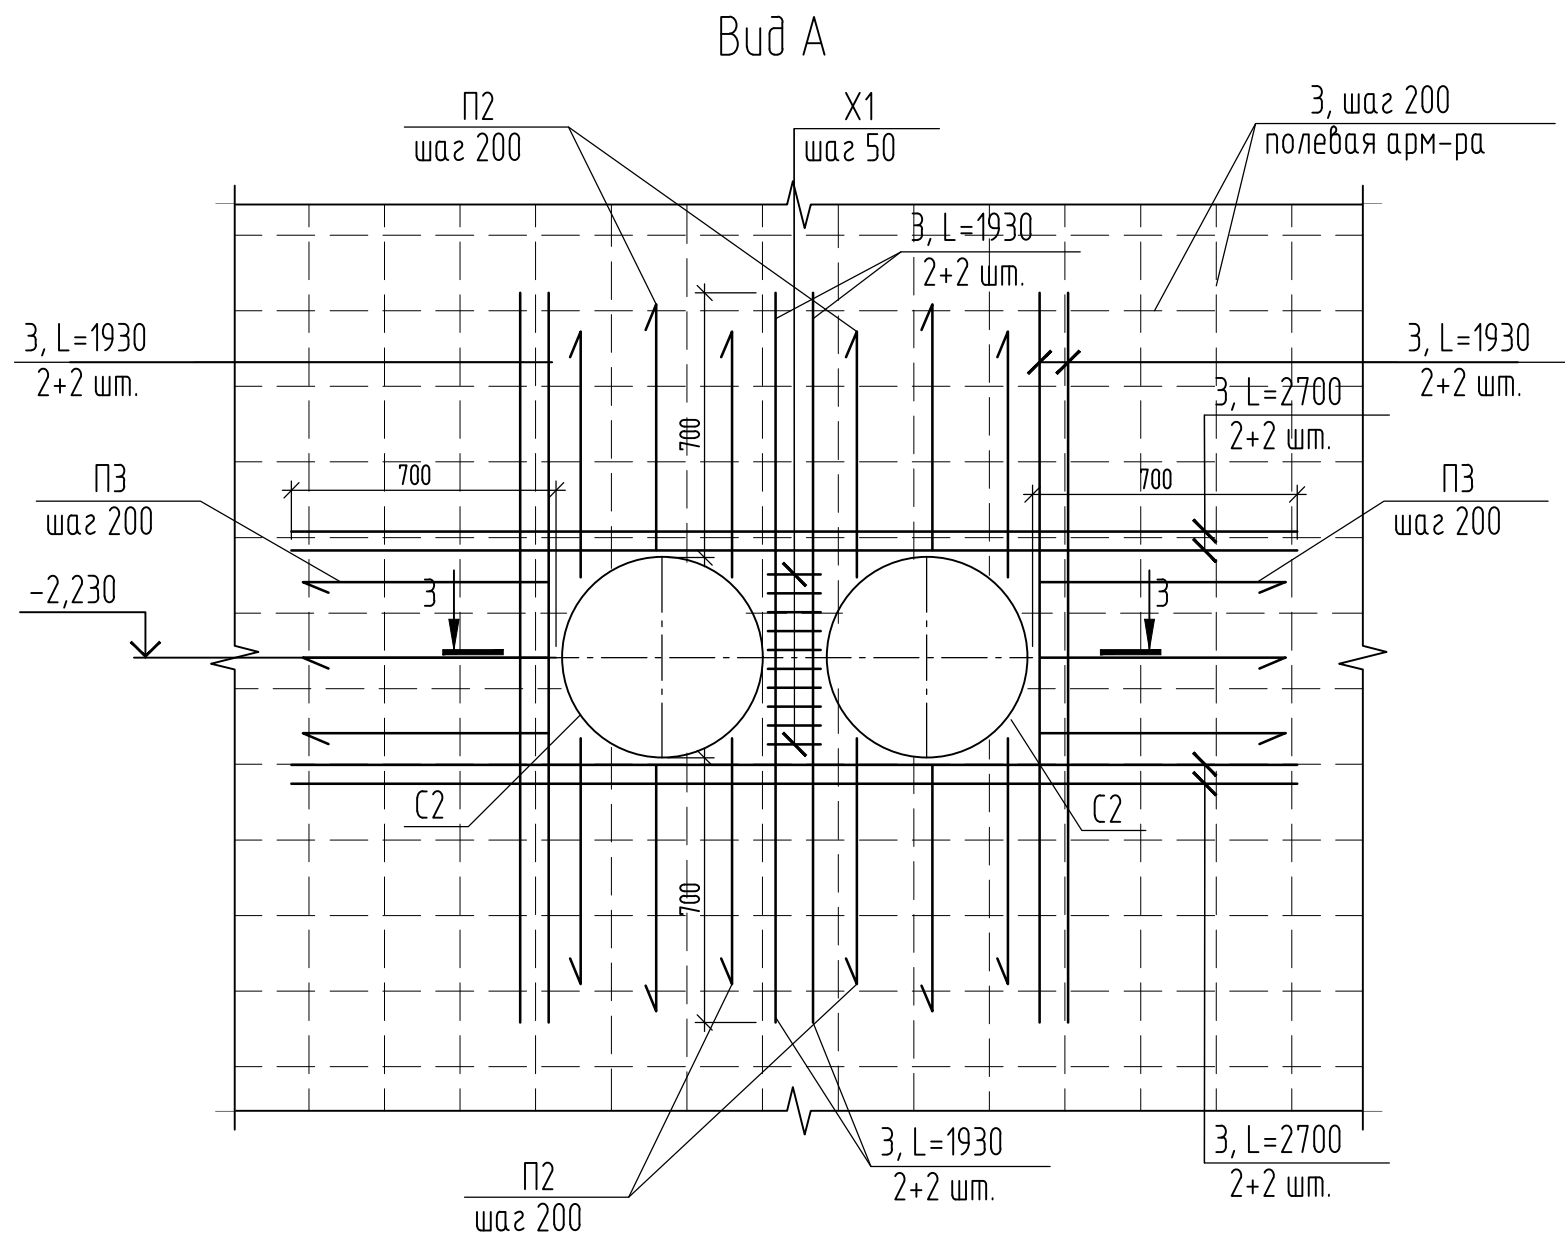


Узел установки гильзы

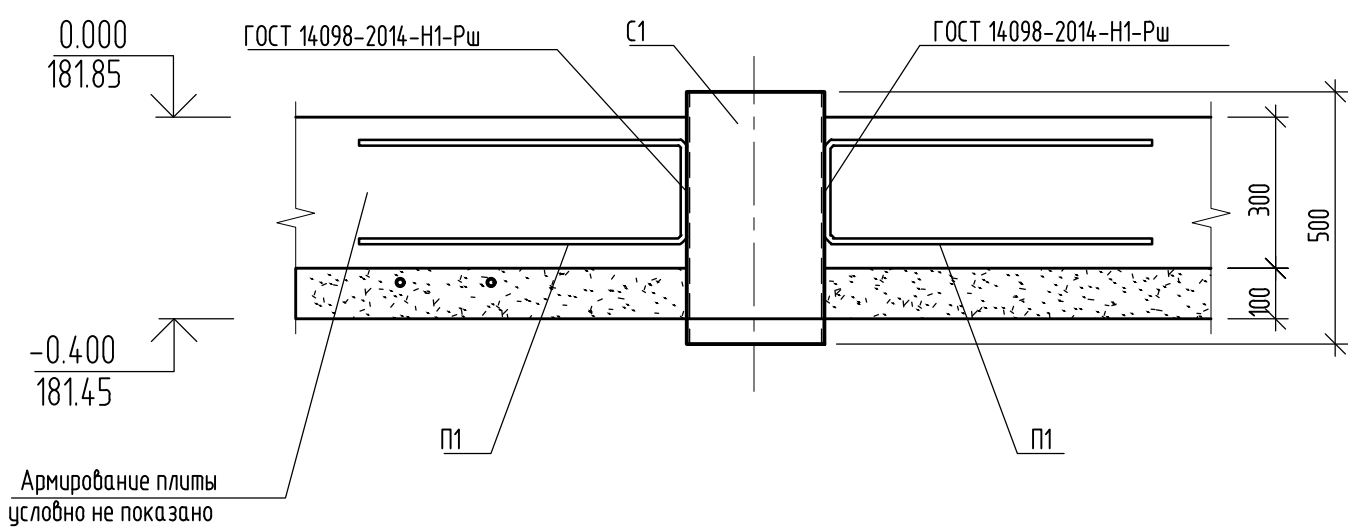


- Под плитой выполнить бетонную подготовку из бетона кл. В7.5 толщиной 100 мм, выходящую за контуры подошвы фундамента на 100 мм.
- Все бетонные и железобетонные конструкции, соприкасающиеся с грунтом, окрасить горячим битумом в два слоя.
- Арматурные стержни в монолитных железобетонных конструкциях во всех пересечениях соединять вязальной проволокой диаметром 1-1,5 мм. Допустимо соединение стержней сваркой. Тип соединений - КЗ-Рп по ГОСТ 14098-2014.
- Количество арматуры поз.1 посчитано с учетом нахлеста (700мм). При армировании не допускается стыкование более 50% сечений стержней. Обязательно выполнять разбежку нахлесточных соединений.
- По периметру здания выполнить отмостку. Устройство отмостки и ведомость расхода материалов см. на л.5.

						4377/2025-Р-КЖ.4		
						Логистический комплекс, расположенный по адресу: город Москва, Краснопахорское поселение, вблизи деревни Софьино		
Изм.	Кол. уч.	Лист	№ док.	Подп.	Дата	Логистический комплекс. Новое строительство	Страница	Лист
Разработчик	Красильников	Минскариб					Р	3
Руч. эр.						Передан через диспетчера 18.08.2025 13:59 СМТ+03:00		
Н. контр.						5b403495-827b-4846-9639-bb4988d9b80		
ГИП	Султанов				2025	Плита монолитная ПМ-1		


Ростверк Р-1
(опалубка)

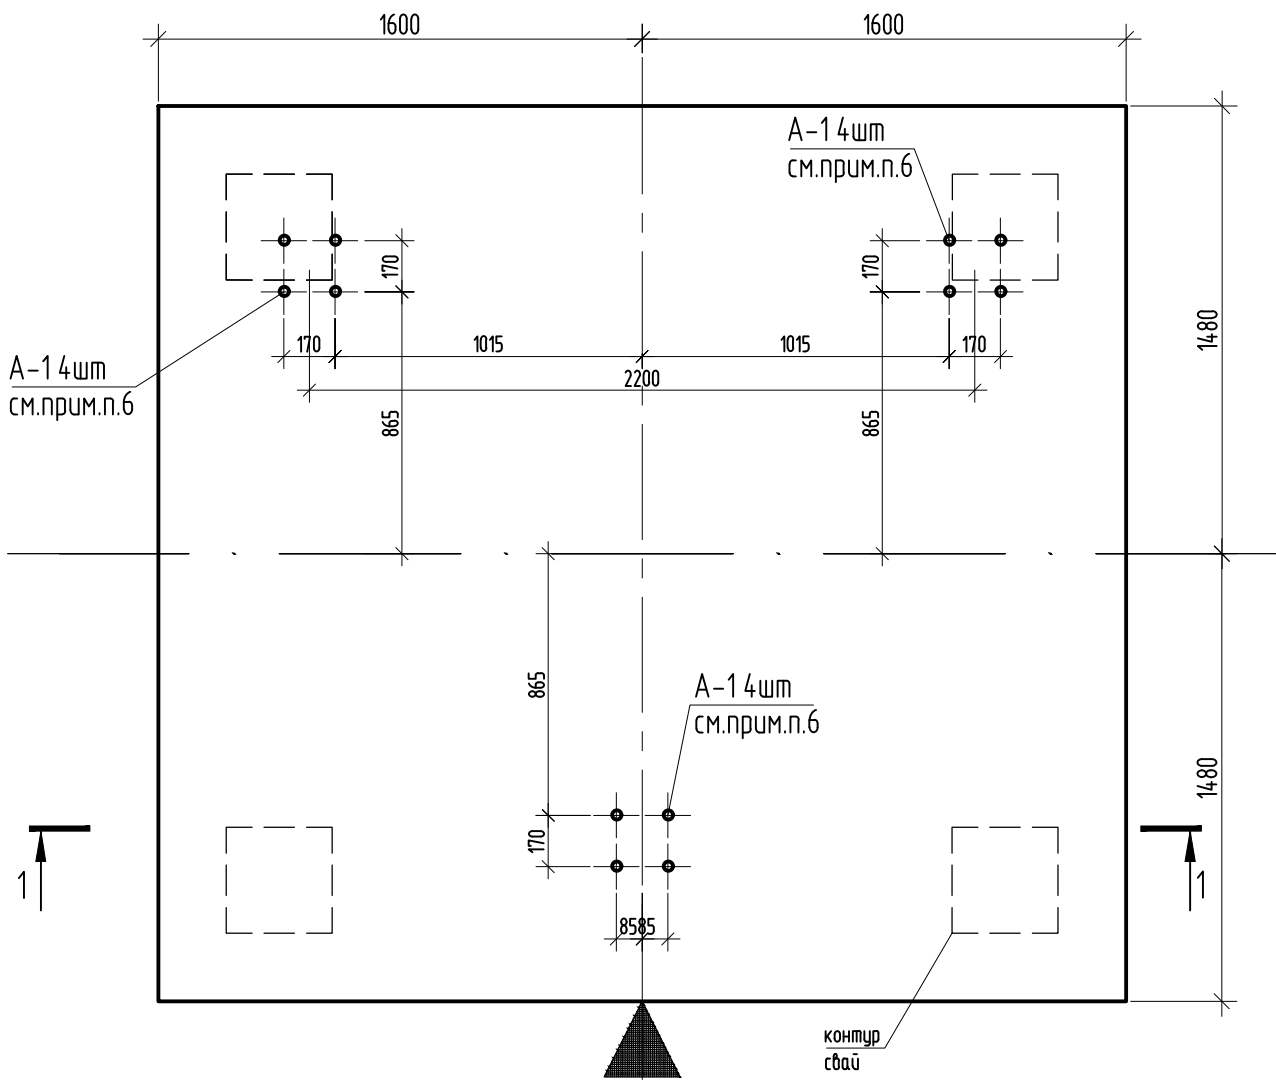

Ростверк Р-1
(армирование нижней зоны)

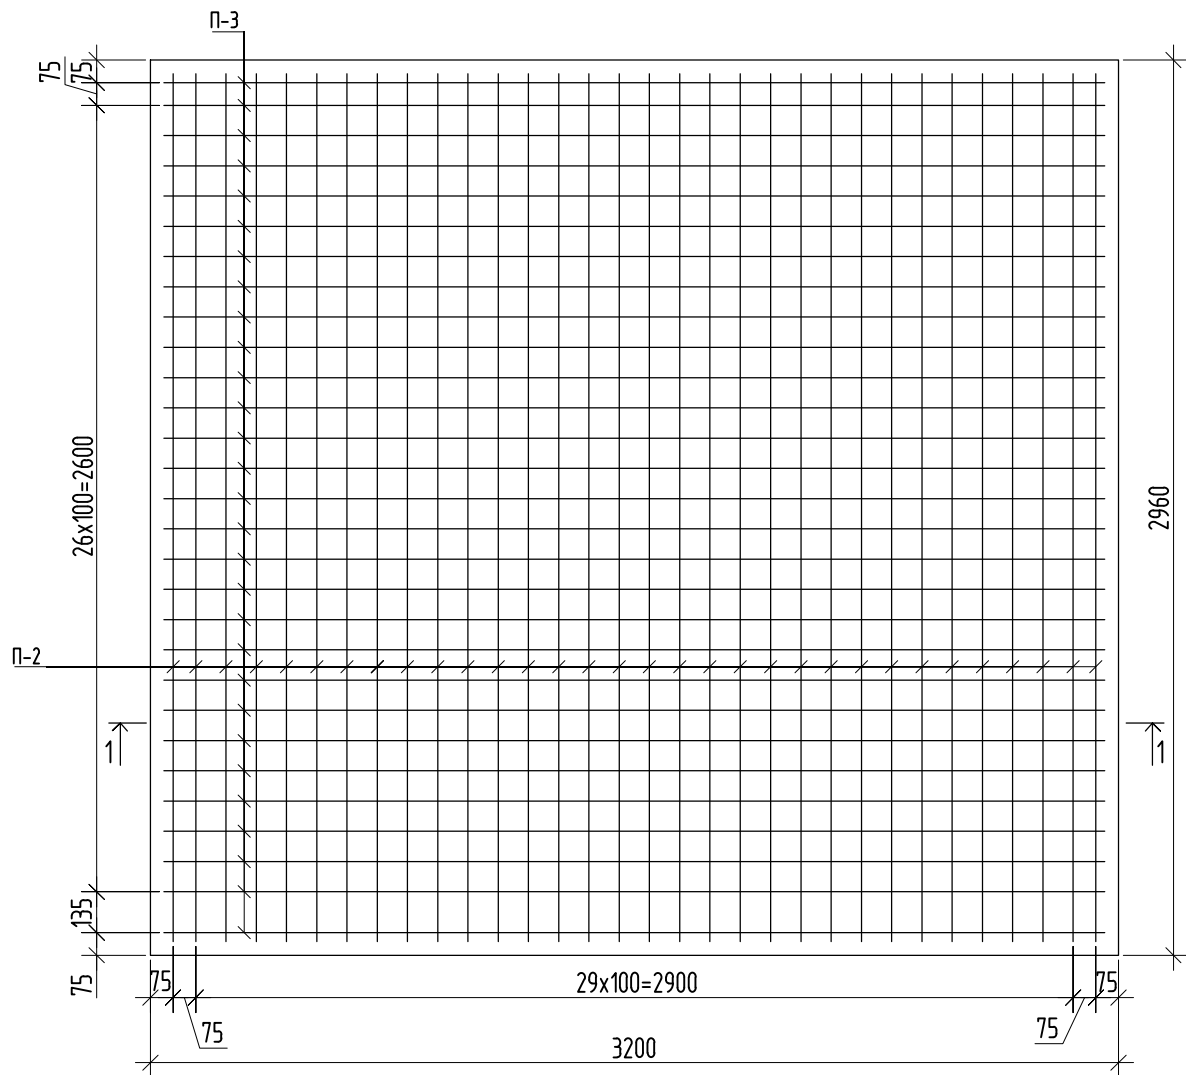


Ростверк Р-1
(армирование верхней зоны)

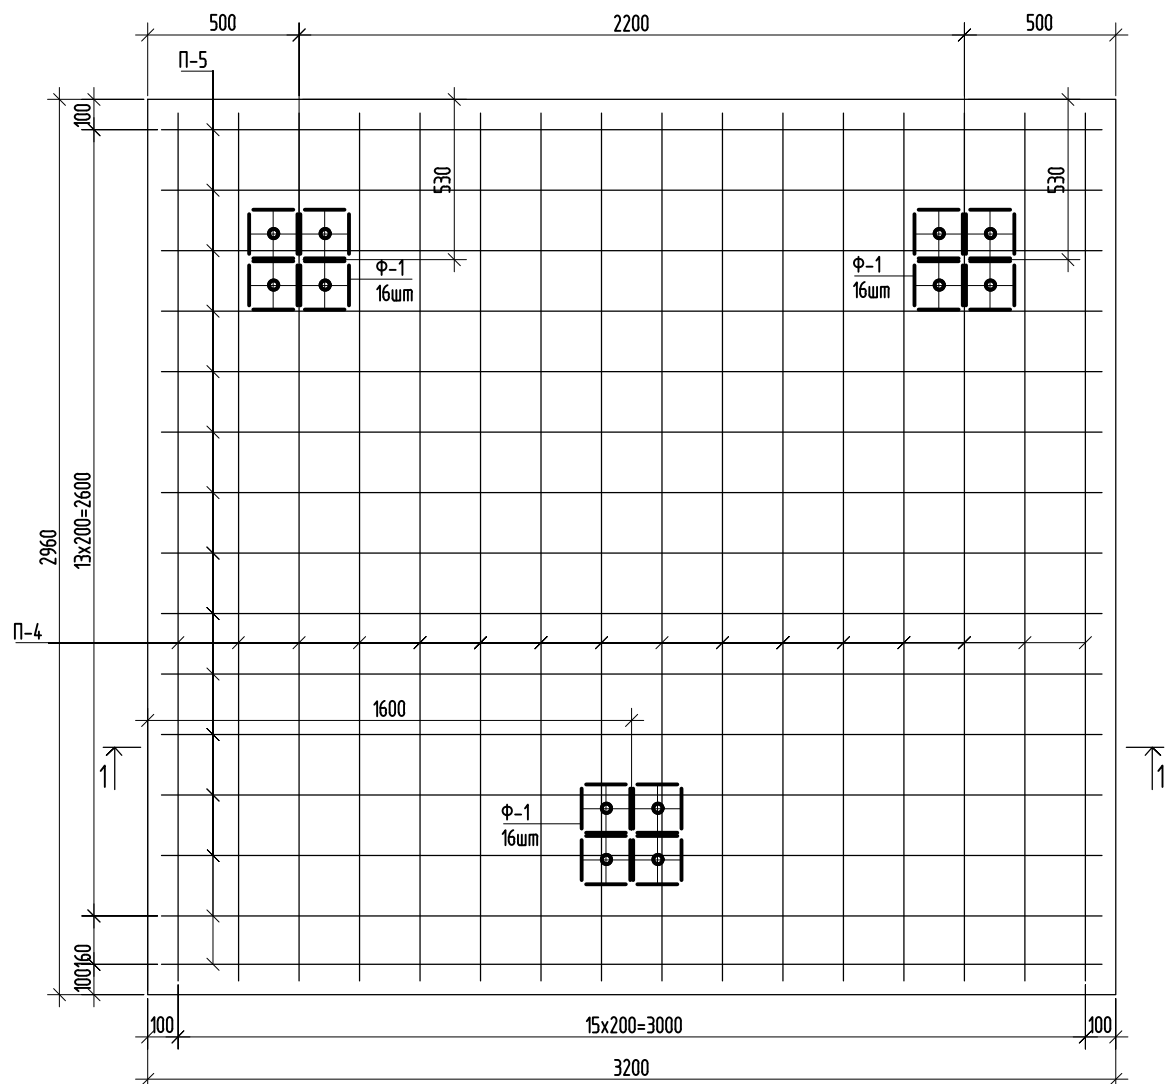


*арматурные стержни попадающие фундаментные болты сместить


1 - 1 (опалубка)

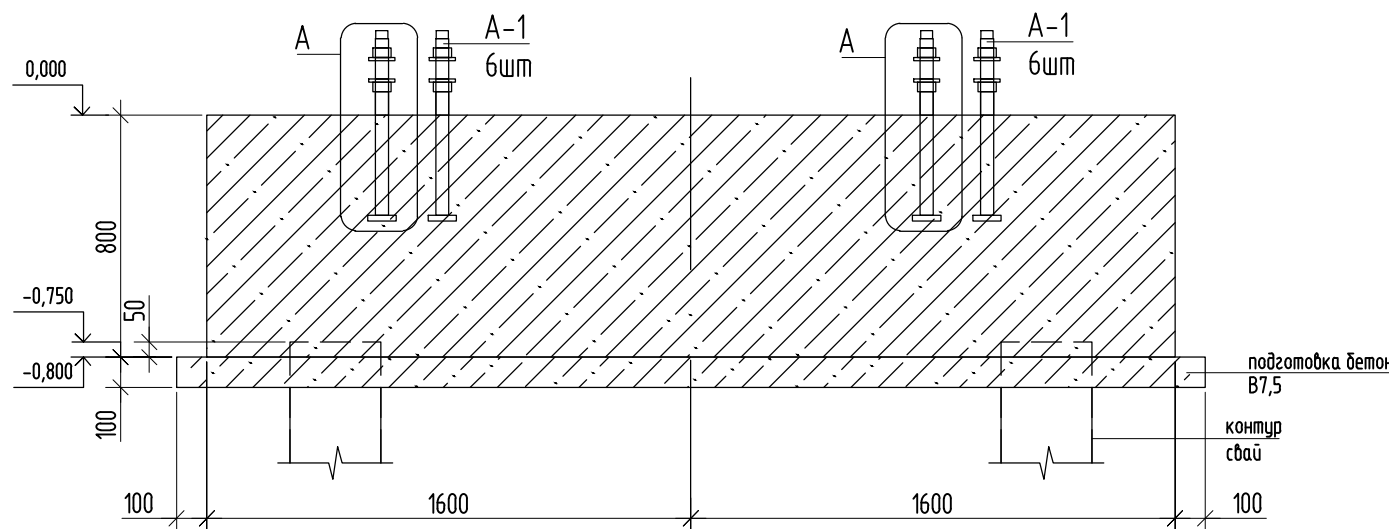

1 - 1 (армирование)

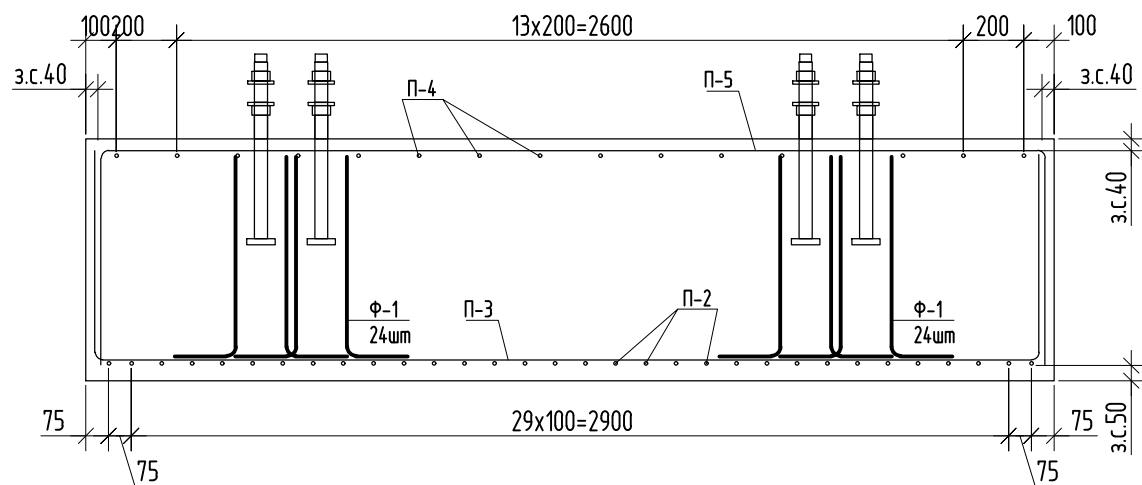

А

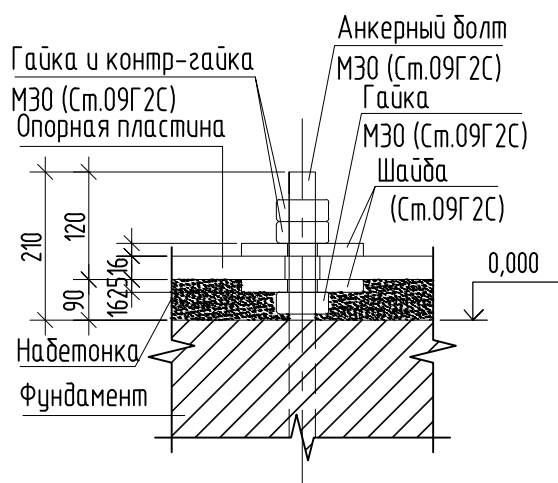

Спецификация на ж/б монолитный ростверк Р-1

Поз.	Обозначение	Наименование	Кол.	Масса ед., кг.	Примечание
П-2	ГОСТ 34028-2016	φ20 А500 L=4200	32	10.36	331.52
П-3	ГОСТ 34028-2016	φ20 А500 L=4440	29	10.95	317.55
П-4	ГОСТ 34028-2016	φ12 А500 L=4200	16	3.73	59.68
П-5	ГОСТ 34028-2016	φ12 А500 L=4440	15	3.94	59.10
Ф-1	ГОСТ 34028-2016	φ12 А500 L=1870	54	1.66	89.64
А-1	ГОСТ 24379.1-2012	Болт М2.1 М30х890 Ст.09Г2С (см. прим. п.6)	12		
		Материалы			
		Обмазочная гидроизоляция	м²	19.0	
		Бетон В30 W6 F150	м³	7.5	
		Бетон В7.5	м³	1.1	


Ведомость деталей

Поз.	Эскиз
П-2	
П-3	
П-4	
П-5	
Ф-1	


-Размеры даны по наружным граням

- Общие данные см. л.1.
- Арматурные выпуски из свай на сечениях условно не показаны.
- До бетонирования обеспечить надежную фиксацию анкерных болтов в проектное положение любым доступным способом. Допуск рамы с болтами в плане ±10мм. Допуск между болтами в раме ±3мм. Допуск по высоте рамы с болтами ±15мм.
- Не допускается разуплотнение и промерзание грунтов под основанием ростверков.
- Поверхности ростверка контактирующие с грунтом обратной засыпки обмазать битумной мастикой за два раза по подготовленной поверхности.
- Марку анкерных болтов уточнить в разделе конструкций трубы дымоудаления.
- Размеры со знаком ""*"" уточнить по месту".


ОП-1

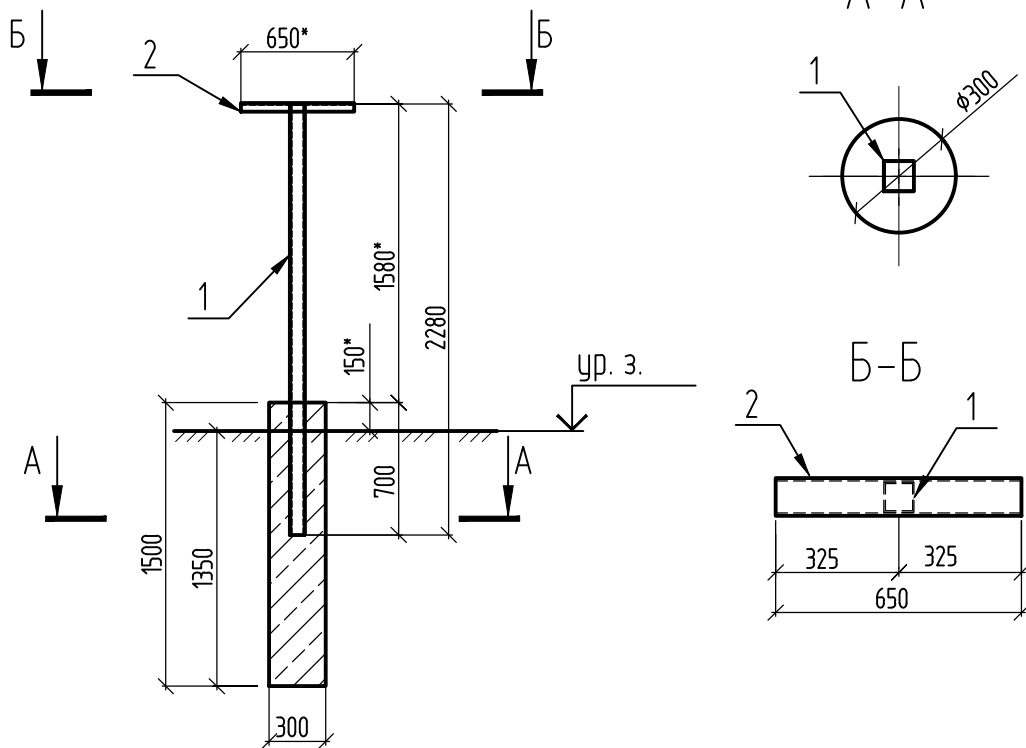

А-А

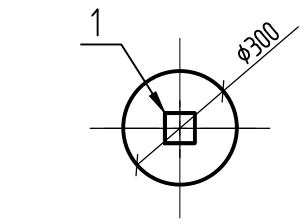

Б-Б

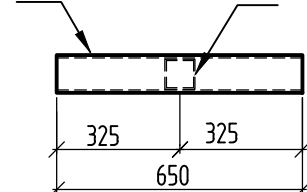

4377/2025-Р-КЖ5.4

Логистический комплекс, расположенный по адресу: город Москва, Краснопахорское поселение, вблизи деревни Софьино


Изм.	Кол. уч.	Лист	№ док.	Подп.	Дата	Стадия	Лист	Листов
Разраб.	Красильников					Р	4	
Проверил	Минсагиров							
Рук. гр.								
Н. контр.								
ГИП	Сулейманов				2025			

Схема расположения ростверка Р-1. Опора ОП1


Передан через Диадок 18.08.2025 13:59 GMT+03:00
5b40d4f5-e21b-4846-9639-bd4998dea8b0
Страница 9 из 15




Закладная деталь ЗД-1

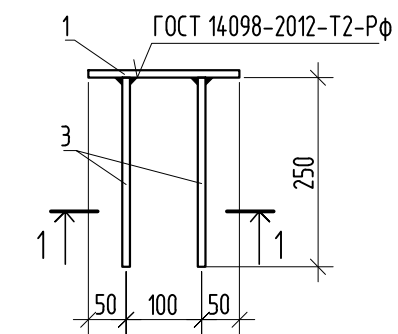


1 - 1

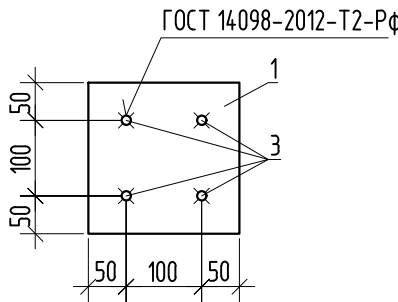


Закладная деталь ЗД-2

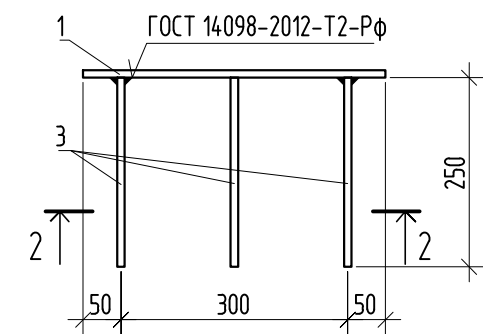

2 - 2

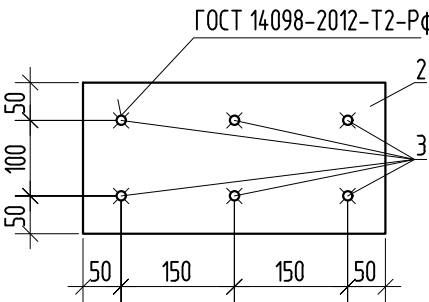

Узел по устройству отмостки здания

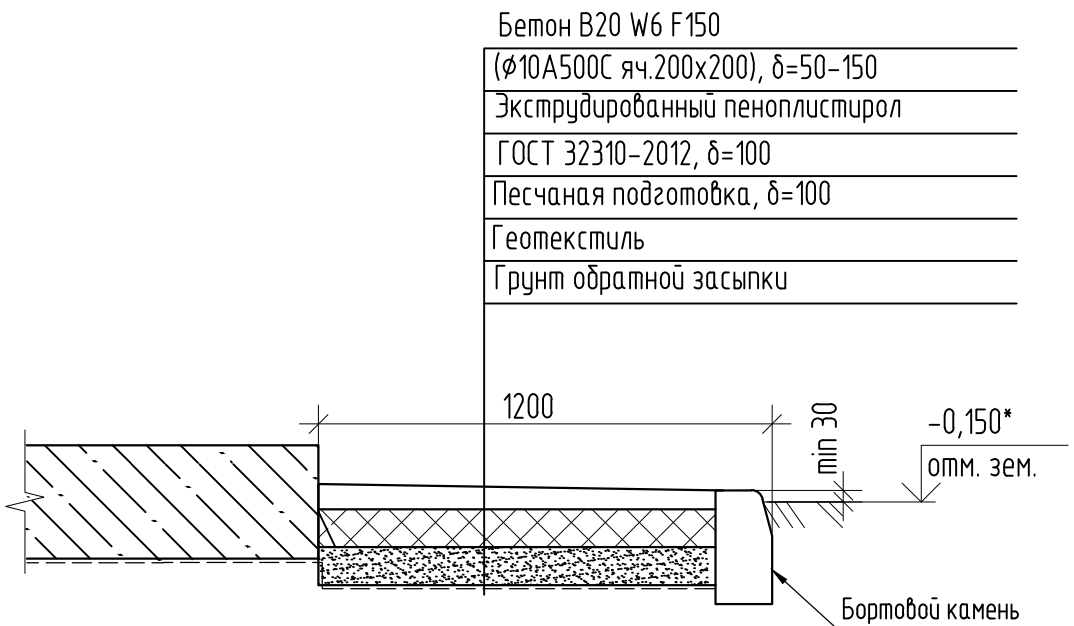

Спецификация на ЗД-1

Поз.	Обозначение	Наименование	Кол.	Масса ед.,кг.	Примечание
1	ГОСТ 19903-2015	- 10x200x200	1	3,14	3.14
3	ГОСТ 34028-2016	φ12 А500С L=250	4	0.22	0.88

Спецификация на ЗД-2

Поз.	Обозначение	Наименование	Кол.	Масса ед.,кг.	Примечание
2	ГОСТ 19903-2015	- 10x200x400	1	6,28	6.28
3	ГОСТ 34028-2016	φ12 А500С L=250	6	0.22	1.32

Спецификация на отмостку

Поз.	Обозначение	Наименование	Кол.	Масса ед.,кг	Прим.
		Сборные единицы			
	ГОСТ 6665-91	БР 100.30.15	78	100	
		Армирование			
	ГОСТ 34028-2016	10-А500С L=780.0	-	481	п.м.
		Материалы			
	ГОСТ 26633-2015	Бетон класса В20, F150, W6	8.6		м³
	ГОСТ 32310-2012	Экструдированный пенополистирол	8.6		м³
		Геотекстиль	85.8		м²
		Песок	8.6		м³

4377/2025-Р-КЖ5.4

Логистический комплекс, расположенный по адресу: город Москва, Краснопахарское поселение, вблизи деревни Софьино

Изм.	Кол. уч.	Лист	№ док.	Подп.	Дата	Стадия	Лист	Листов
Разраб.		Красильников				Р	5	
Проверил		Минсагиров						
Рук. гр.								
Н. контр.								
ГИП		Сулейманов						
					2025			

Закладные детали ЗД-1, ЗД-2.
Устройство отмостки

Передан через Диадок 18.08.2025 13:59 GMT+03:00
5b40d4f5-e21b-4846-9639-bd4998dea8b0
Страница 10 из 15



ЛОКАЛЬНЫЙ СМЕТНЫЙ РАСЧЕТ

№ п/ п	Наименование работ и затрат	Ед. изм.	Кол-во	Материалы		Работы		Всего (в руб., в т.ч. НДС 20%)
				Цена за ед. (в руб., в т.ч. НДС 20%)	Итого (в руб., в т.ч. НДС 20%)	Цена за ед. (в руб., в т.ч. НДС 20%)	Итого (в руб., в т.ч. НДС 20%)	
	<u>Устройство фундаментной плиты с приямком под котельную</u>							0
1	Бетон В7,5	м3	18,00	7 500,00	135 000,00	6 500,00	117 000,00	252 000,00
2	Обмазочная гидроизоляция в 1 слой	м2	208,00	360,00	74 880,00	250,00	52 000,00	126 880,00
3	Бетон В25 F150 W6	м3	56,50	8 000,00	452 000,00	20 000,00	1 130 000,00	1 582 000,00
4	Арматура А500С ГОСТ 34028-2016 Ø16 мм	тн	1,781	58 000,00	103 298,00	15 000,00	26 715,00	130 013,00
5	Арматура А500С ГОСТ 34028-2016 Ø14 мм	тн	4,829	58 000,00	280 082,00	15 000,00	72 435,00	352 517,00
6	Арматура А500С ГОСТ 34028-2016 Ø8 мм	тн	0,241	58 000,00	13 978,00	15 000,00	3 615,00	17 593,00
7	Арматура А500С ГОСТ 34028-2016 Ø6 мм	тн	0,027	58 000,00	1 566,00	15 000,00	405,00	1 971,00
8	Закладные детали	тн	0,193	1 200 000,00	231 600,00	250 000,00	48 250,00	279 850,00
9	Гильза ø57х3,0	тн	0,002	1 200 000,00	2 400,00	250 000,00	500,00	2 900,00
10	Гильза ø114х3,0	тн	0,008	3 195 000,00	25 560,00	250 000,00	2 000,00	27 560,00
11	Гильза ø152х5,0	тн	0,009	8 000 000,00	72 000,00	250 000,00	2 250,00	74 250,00
12	Гильза ø159х5,0	тн	0,010	1 000 000,00	10 000,00	250 000,00	2 500,00	12 500,00
13	Гильза ø180х5,0	тн	0,022	5 300 000,00	116 600,00	250 000,00	5 500,00	122 100,00
14	Гильза ø530х7,0	тн	0,062	860 000,00	53 320,00	250 000,00	15 500,00	68 820,00
	<u>Устройство Ростверка Р1 и опоры Оп-1</u>							0,00
1	Срубка свай в отметку с утилизацией	шт	4	40 000,00	160 000,00	50 000,00	200 000,00	360 000,00
2	Бетон В7,5	м3	1,10	7 500,00	8 250,00	6 500,00	7 150,00	15 400,00
3	Обмазочная гидроизоляция в 1 слой	м2	19,00	360,00	6 840,00	250,00	4 750,00	11 590,00
4	Бетон В25 F150 W6	м3	7,50	8 000,00	60 000,00	20 000,00	150 000,00	210 000,00
5	Арматура А500С ГОСТ 34028-2016 Ø20 мм	тн	0,650	58 000,00	37 700,00	15 000,00	9 750,00	47 450,00
6	Арматура А500С ГОСТ 34028-2016 Ø12 мм	тн	0,210	58 000,00	12 180,00	15 000,00	3 150,00	15 330,00
7	Болты 2.1 М30х890 Ст.09Г2С	шт	12	2 465,00	29 580,00	1 000,00	12 000,00	41 580,00
8	Труба 80х4	тн	0,042	575 000,00	24 150,00	250 000,00	10 500,00	34 650,00
9	Швеллер 10П	тн	0,011	580 000,00	6 380,00	250 000,00	2 750,00	9 130,00
	<u>Прочее</u>							0,00
1	Разработка грунта, перемещение в пределах строительной площадки	м3	77	828,00	63 756,00			63 756,00

Передан через Диадок 18.08.2025 13:59 GMT+03:00
1 000,9b40d4f5-e21b-4846-96b9-4bd4998dea8b040 756,00

2	Обратная засыпка	м3	32,0	3 400,00	108 800,00	1 500,00	48 000,00	156 800,00
3	Мобилизация и демобилизация подрядчика и оборудования	компл.	1	80 360,00	80 360,00	20 000,00	20 000,00	100 360,00
	Итого:				2 170 280,00		2 023 720,00	4 194 000,00
							В т.ч. НДС (20%)	699 000,00



ГРАФИК ПРОИЗВОДСТВА РАБОТ

Вид работ	Год:2025																															
	01.09.2025	02.09.2025	03.09.2025	04.09.2025	05.09.2025	06.09.2025	07.09.2025	08.09.2025	09.09.2025	10.09.2025	11.09.2025	12.09.2025	13.09.2025	14.09.2025	15.09.2025	16.09.2025	17.09.2025	18.09.2025	19.09.2025	20.09.2025	21.09.2025	22.09.2025	23.09.2025	24.09.2025	25.09.2025	26.09.2025	27.09.2025	28.09.2025	29.09.2025	30.09.2025	01.10.2025	
Разработка грунта, перемещение в пределах строительной площадки	6	6																														
Обратная засыпка			6	6																												
Бетонная подготовка					6																											
Обмазочная гидроизоляция в 1 слой										2	2																					
Армирование						6	6	6	4	4	6	6	6	6	6	6	6	6	6													
Монтаж закладных деталей и гильз																				6	6	6	6	6								
Монтаж опалубки, укладка бетона в осях 15-30																										6	6	6	6	6	6	6
	6	6	6	6	6	6	6	6	6	6	6	6	6	6	6	6	6	6	6	6	6	6	6	6	6	6	6	6	6	6	6	



ГРАФИК ФИНАНСИРОВАНИЯ

№	Наименование оплаты	Сумма, руб.,	Срок оплаты
1	Аванс	1 258 200,00	В течение 5 (пяти) рабочих дней с момента подписания настоящего дополнительного соглашения и выставления счёта на аванс
2	Оплата по фактическим объемам за вычетом суммы аванса	По факту, за вычетом суммы аванса	В течение 20 (Двадцати) рабочих дней с момента подписания сторонами акта о приемке выполненных работ по форме №КС-2 и Справки о стоимости выполненных работ и затрат по форме №КС-3



АКТ ПРИЕМА-ПЕРЕДАЧИ СТРОИТЕЛЬНОЙ ПЛОЩАДКИ

15.08.2025

Общество с ограниченной ответственностью «ВБ Инжиниринг», именуемое в дальнейшем «Заказчик», в лице генерального директора Куликова Алексея Альбертовича, действующего на основании Устава, с одной стороны, и

Общество с ограниченной ответственностью «МОНТПЛАН», именуемое в дальнейшем «Подрядчик», в лице генерального директора Папуца Александра Ивановича, действующего на основании Устава, с другой стороны, далее именуемые «Стороны», составили настоящий акт (далее – Акт) о нижеследующем:

1. Заказчик передал Подрядчику, а Подрядчик принял строительную площадку для выполнения работ по Соглашению.
2. Подрядчик не имеет претензий к Заказчику по состоянию строительной площадки.
3. Рабочая документация необходимая для выполнения работ, а также геодезическая разбивочная основа получены Подрядчиком.

Заказчик:
ООО «ВБ Инжиниринг»

Подрядчик:
ООО «МОНТПЛАН»

Генеральный директор

_____/ **А.А. Куликов/**
М.П.

Генеральный директор

_____/ **А.И. Папуца/**
М.П.

Идентификатор документа 5b40d4f5-e21b-4846-9639-bd4998dea8b0

Документ подписан и передан через оператора ЭДО АО «ПФ «СБ Контур»

Организация, сотрудник		Доверенность: рег. номер, период действия и статус	Сертификат: серийный номер, период действия	Дата и время подписания
Подписи отправителя:	 ООО "МОНТПЛАН" Папуца Александр Иванович, Генеральный Директор	 Не требуется для подписания	0202CDD60064B229964E2AF440 56EC6B54 с 13.01.2025 15:52 по 13.04.2026 15:52 GMT+03:00	18.08.2025 13:59 GMT+03:00 Подпись соответствует файлу документа
Подписи получателя:	 Общество с ограниченной ответственностью "ВБ Инжиниринг" Володина Ирина Вадимовна Доверитель: Общество с ограниченной ответственностью "ВБ ИНЖИНИРИНГ"	 506772a6-ab71-4b89-8671-c2885dc8b3fa с 27.02.2025 00:00 по 27.02.2028 23:59 GMT+03:00 Доверенность прошла проверку	09D6EF80001DB3C2B543C5A267 EA75683A с 17.07.2025 10:39 по 17.07.2026 10:39 GMT+03:00	19.08.2025 22:37 GMT+03:00 Подпись соответствует файлу документа